

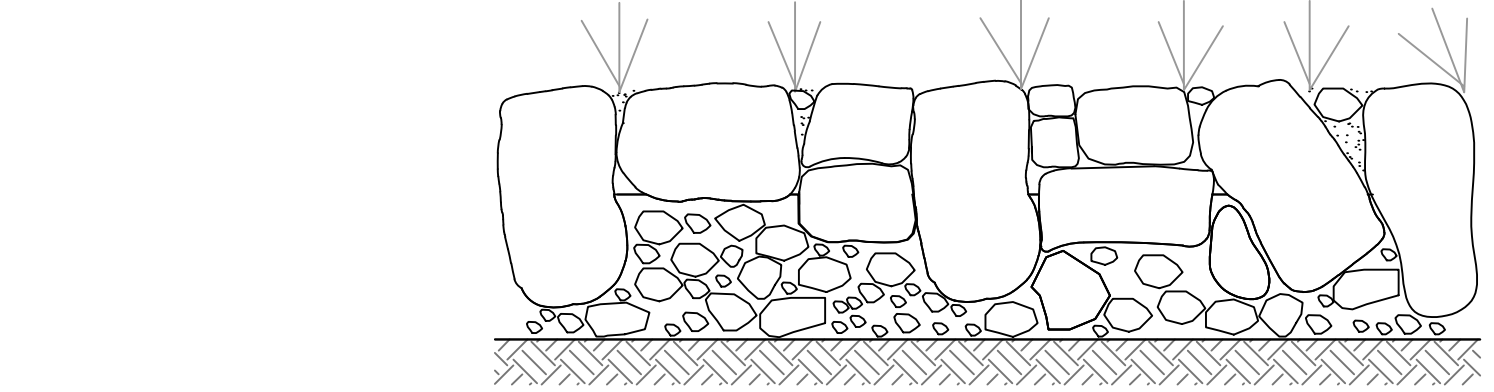
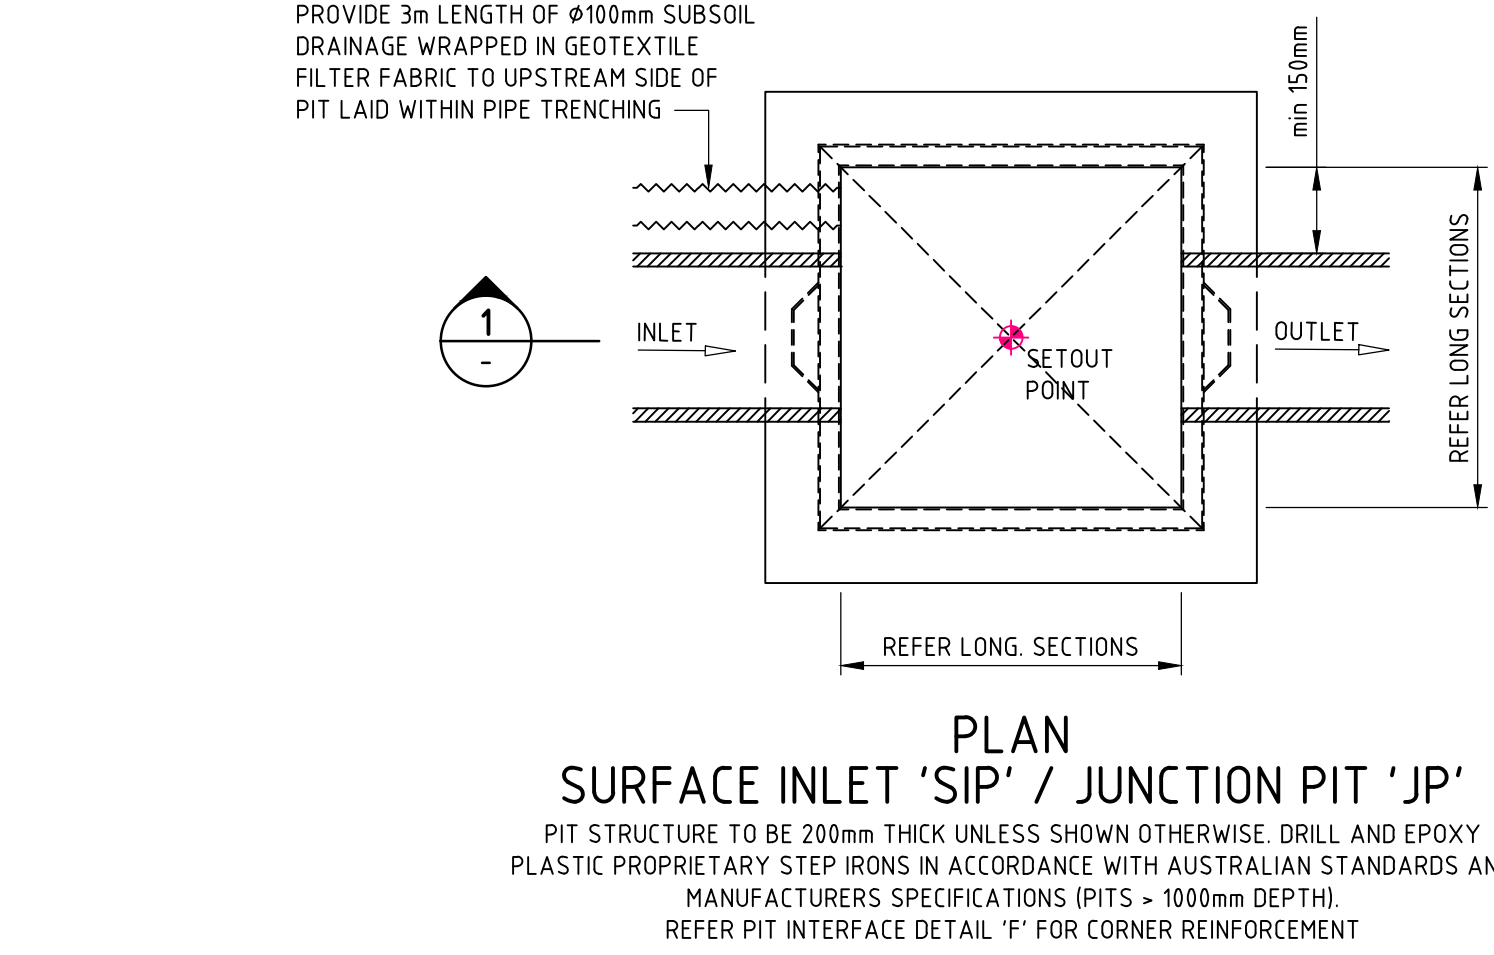
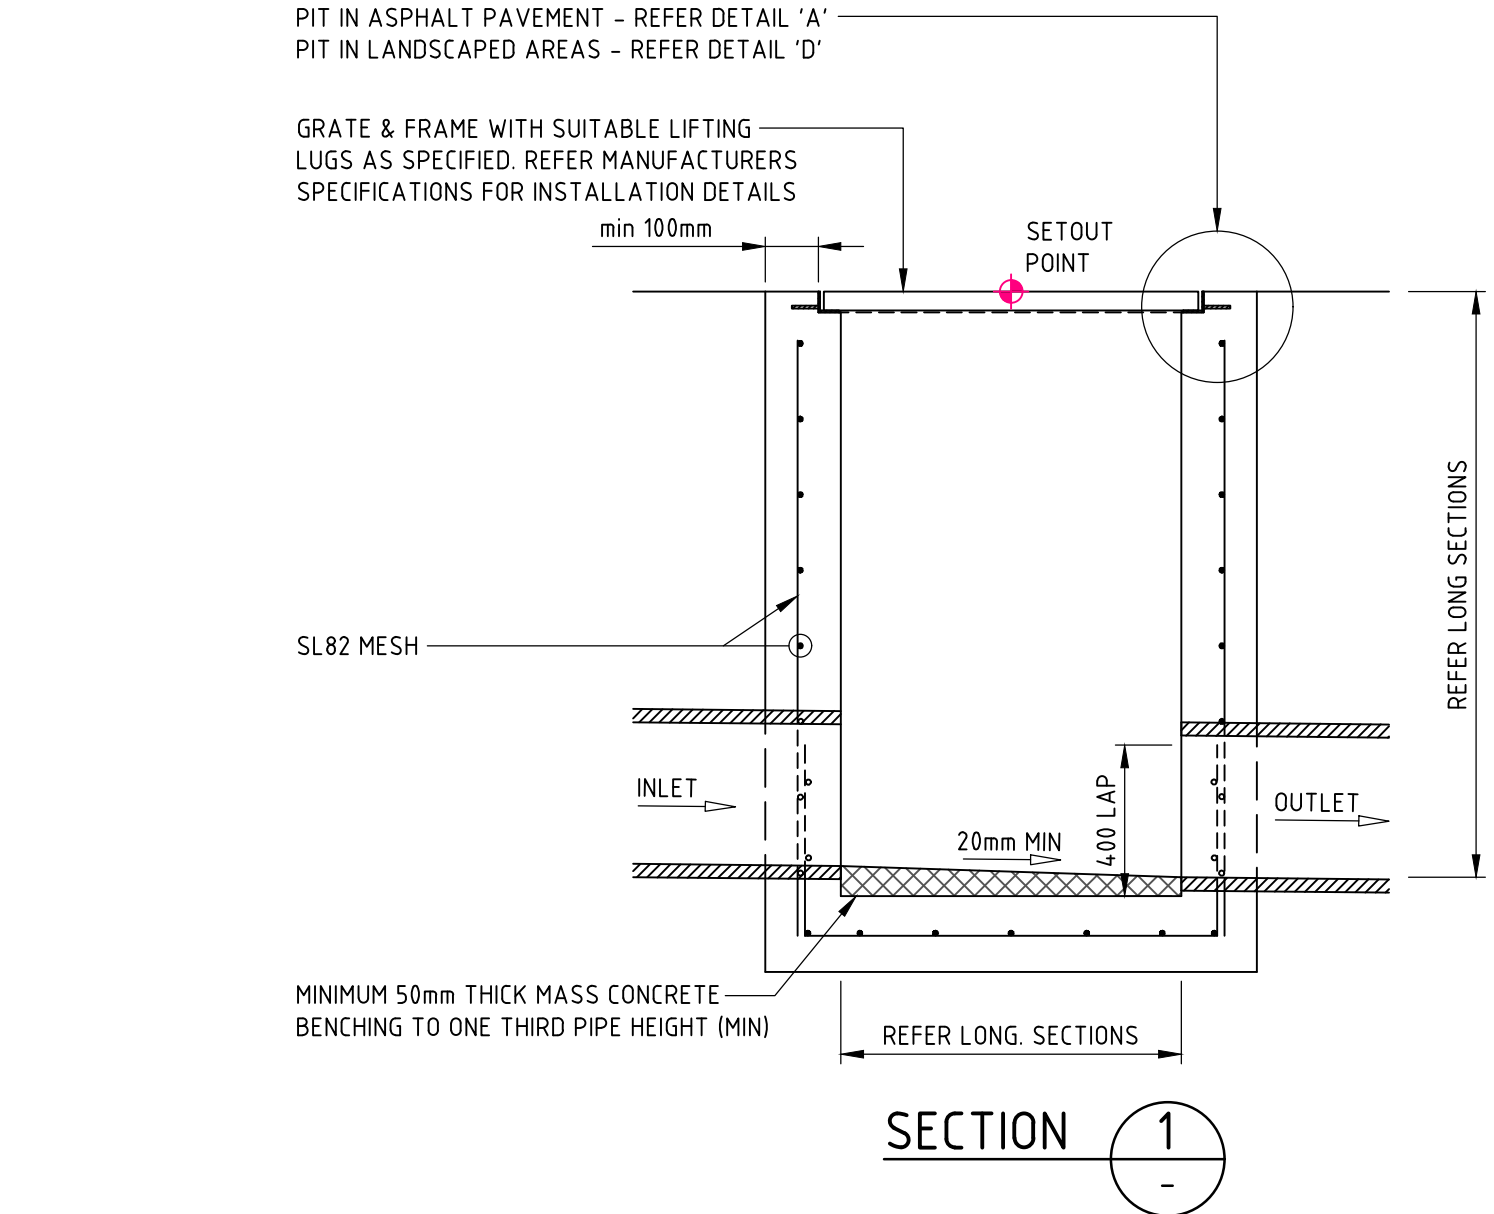
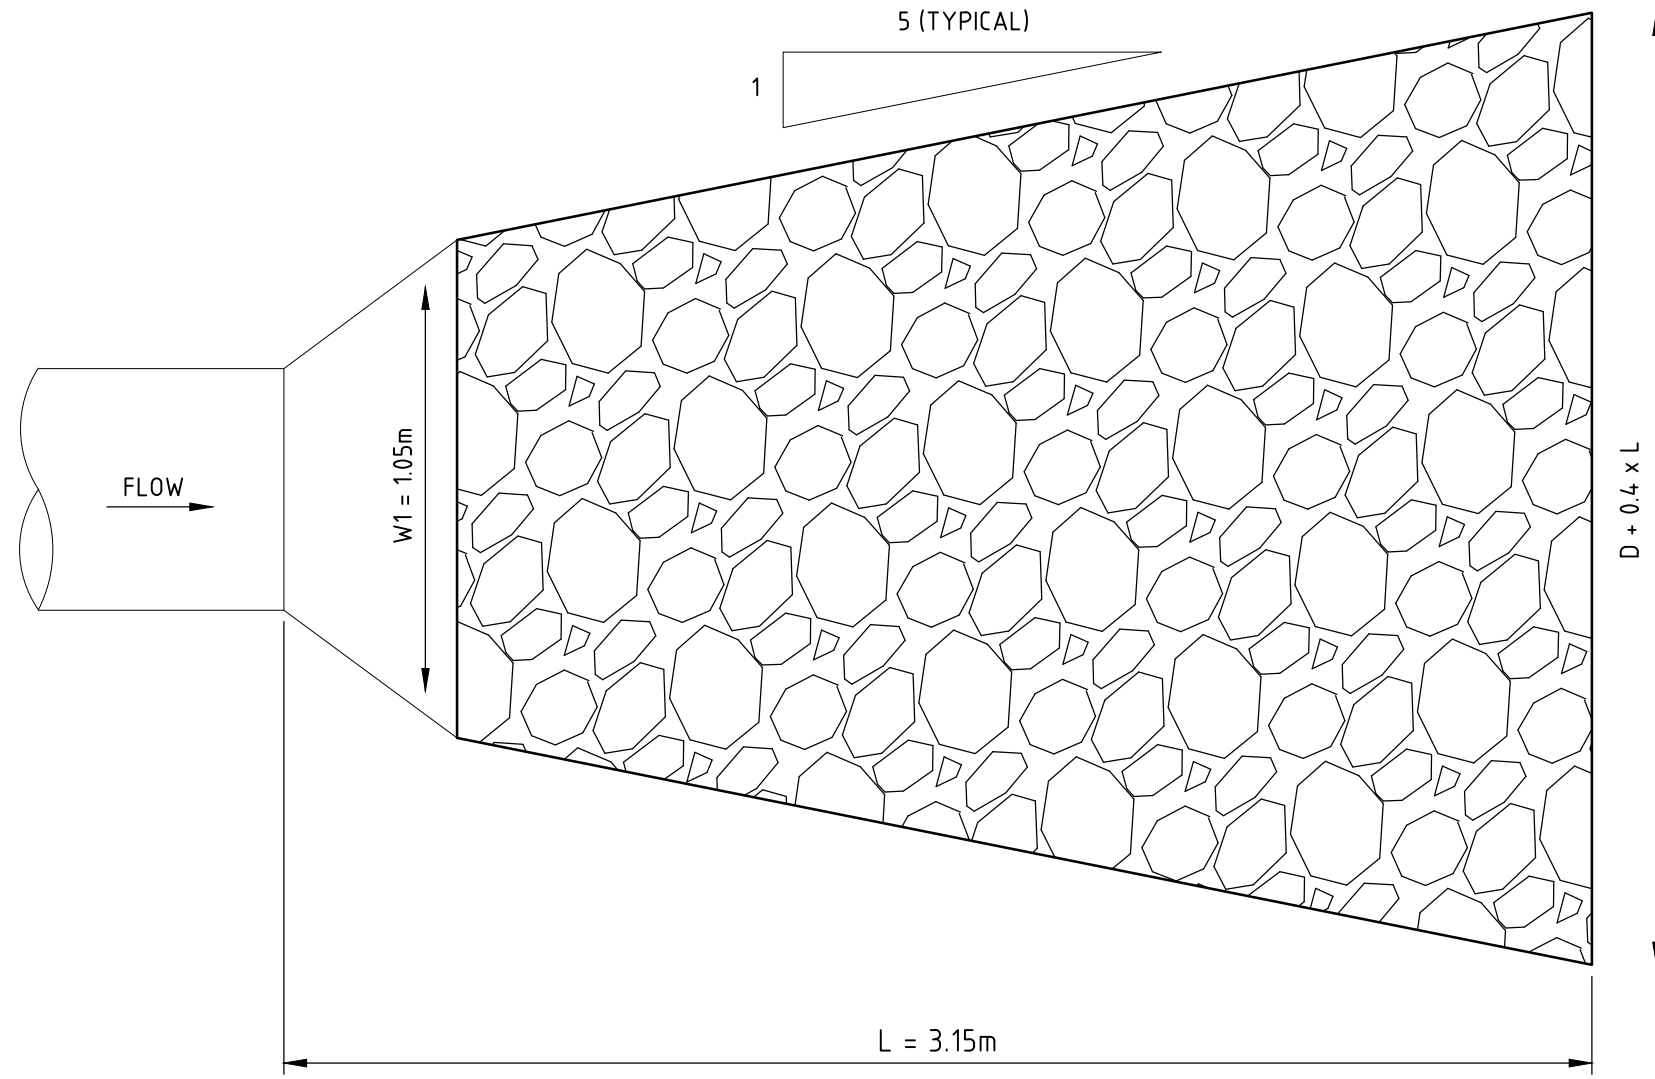
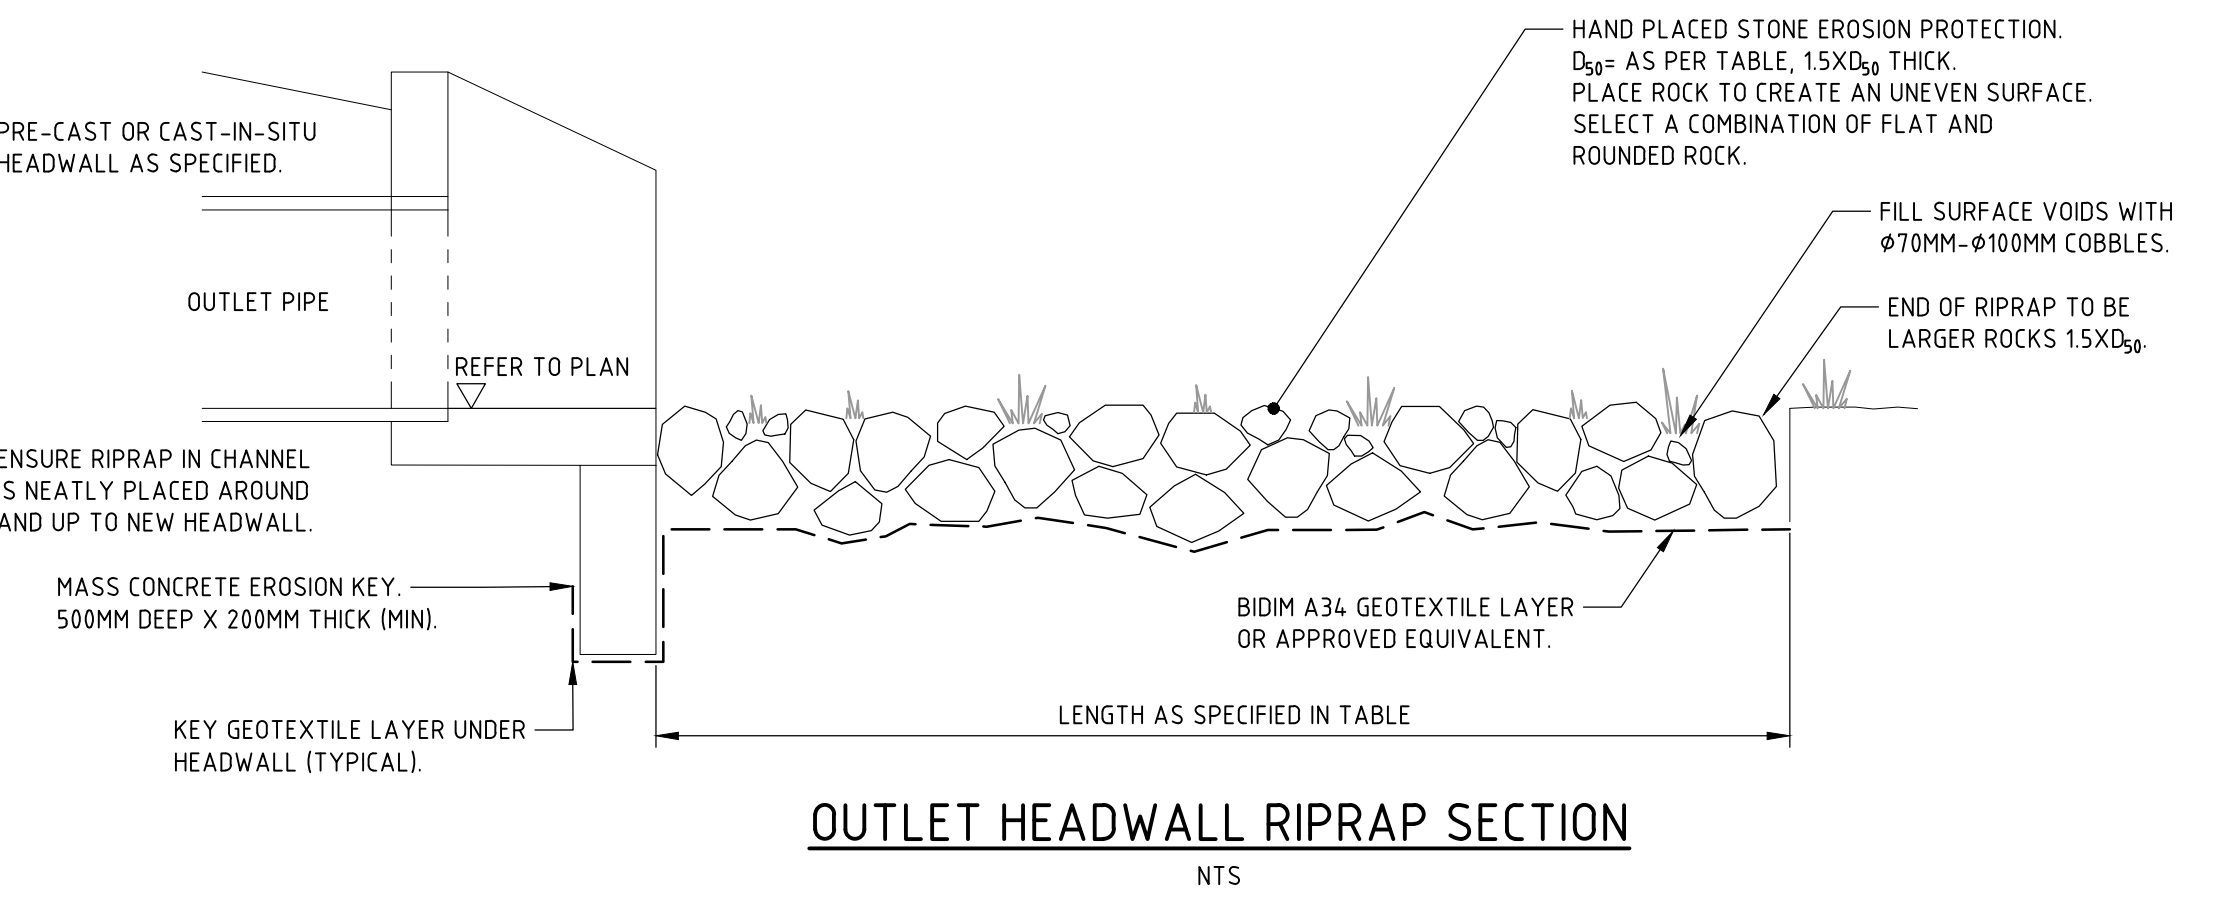
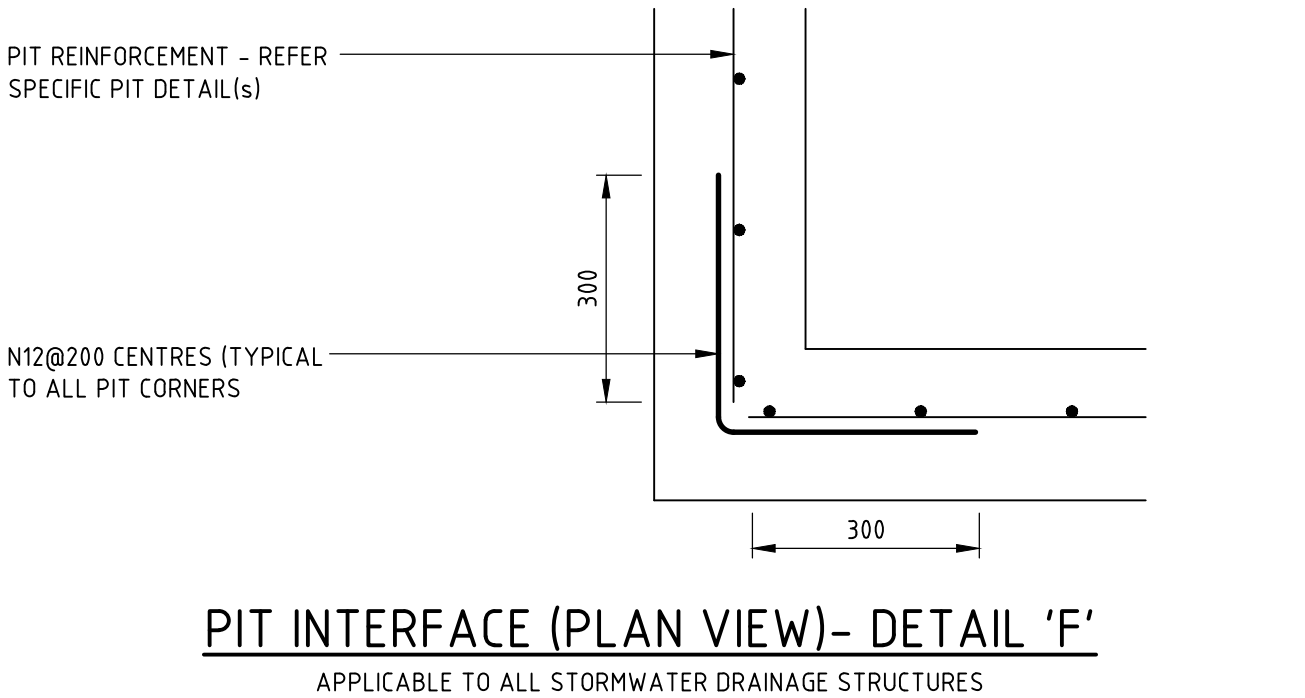


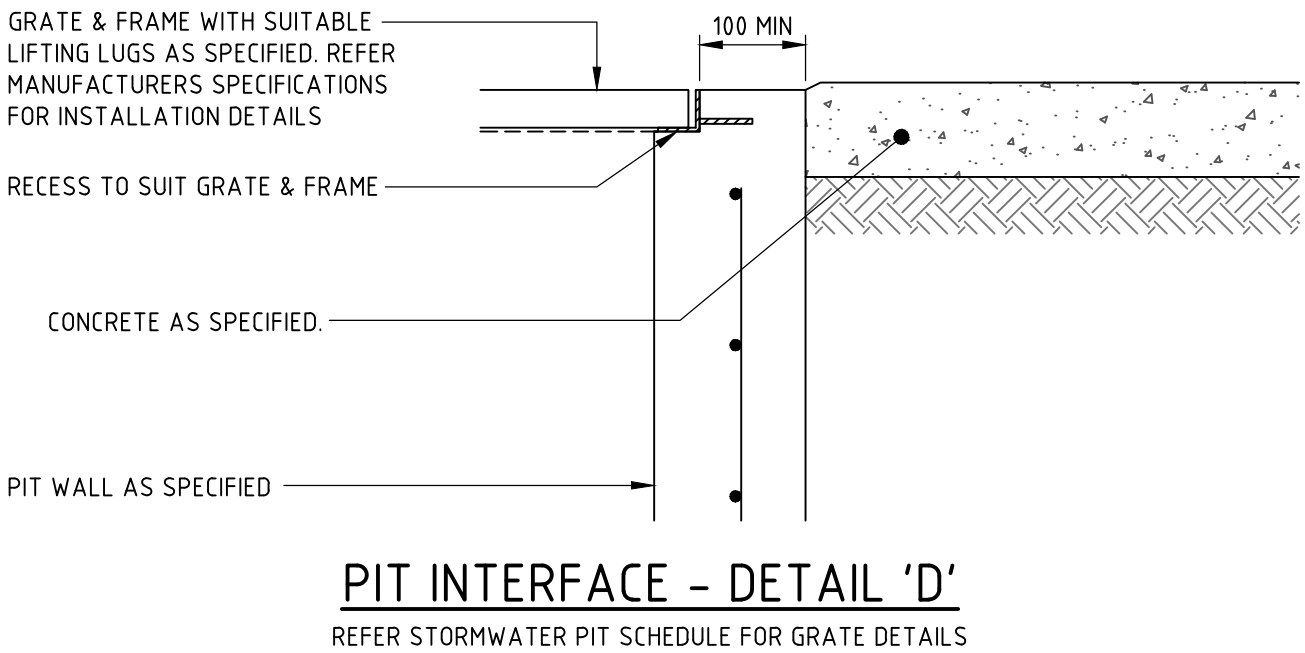

- NOTES:
- ALL RIPRAP MUST CONSIST OF HARD, DURABLE ANGULAR RUN-OF-QUARRY ROCK; RESISTANT TO WEATHERING & WATER ACTION; FREE FROM OVERBURDEN, SPOIL, SHALE & ORGANIC MATERIAL; & SHALL MEET THE GRADATION REQUIREMENTS SPECIFIED.
 - ROUNDED STONES/BOULDERS WILL NOT BE ACCEPTABLE.
 - SHALE AND ROCK WITH SHALE SEAMS WILL NOT BE ACCEPTABLE.
 - ROCKS ARE TO BE PLACED OVER A 200mm LAYER OF ANGULAR COBBLES $D_{50}=140\text{mm}$.
 - ALL ROCK AND COBBLES TO BE PACKED WITH TOPSOIL. GAPS IN RIPRAP TO BE PLANTED WITH SUITABLE NATIVE GRASSES/SEDGES.
 - RIPRAP SHALL BE PLACED ON THE PREPARED SLOPE IN A MANNER THAT WILL PRODUCE A REASONABLY WELL GRADED MASS OF STONE WITH THE MINIMUM PRACTICAL PERCENTAGE OF VOIDS.
 - LARGER STONES SHALL BE WELL DISTRIBUTED & THE ENTIRE MASS OF STONE SHALL CONFORM TO THE GRADATION SPECIFIED BY THE ENGINEERING PLANS.
 - THE MINIMUM THICKNESS OF THE RIPRAP LAYER IS TO BE 1.5 TIMES THE d_{50} ROCK SIZE & NOT BE LESS THAN 300mm FOR PRACTICAL PLACEMENT.
 - THE MINIMUM DENSITY OF STONE USED SHALL NOT BE LESS THAN 2200 kg/cu.m.
- TYPICAL ROCK WEIGHT RANGES FOR RIPRAP ARE:
M50 - 60kg (NOM 300MD)
M15 - 25kg
M100 - 120kg

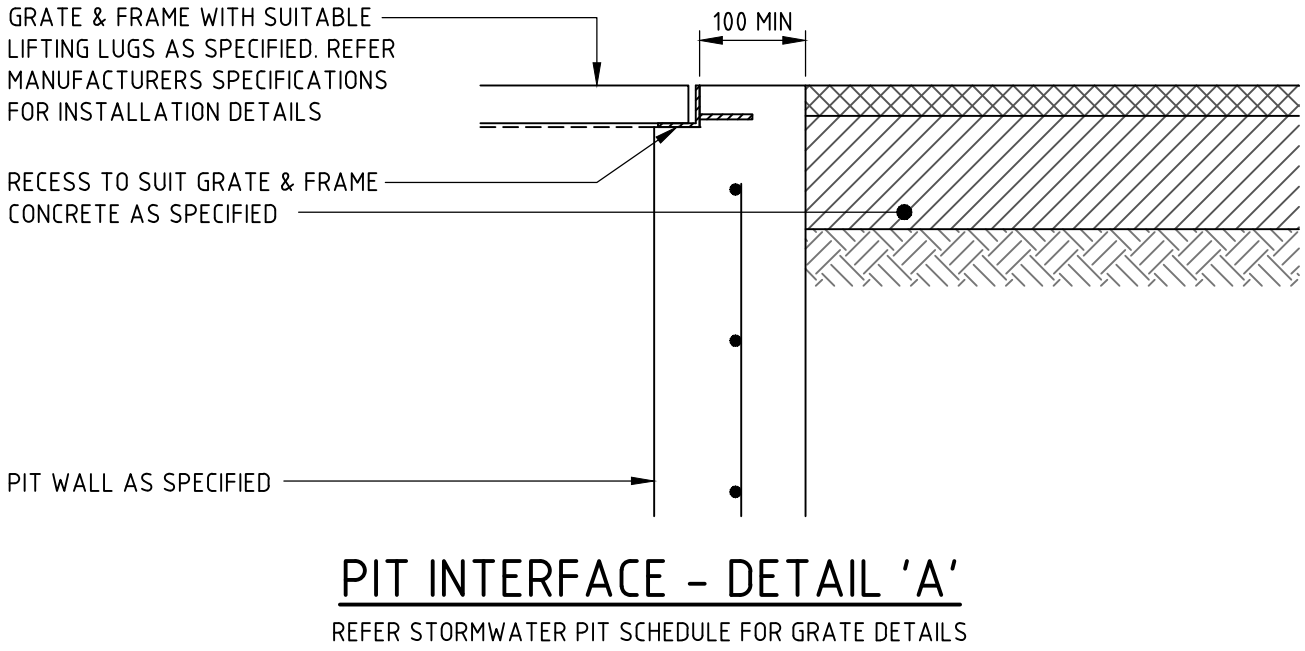

OUTLET ROCK SIZING		
OUTLET NUMBER	ROCK SIZE (d50min)	LENGTH OF ROCK PAD (m)
HW8/1	200mm	3.15m