


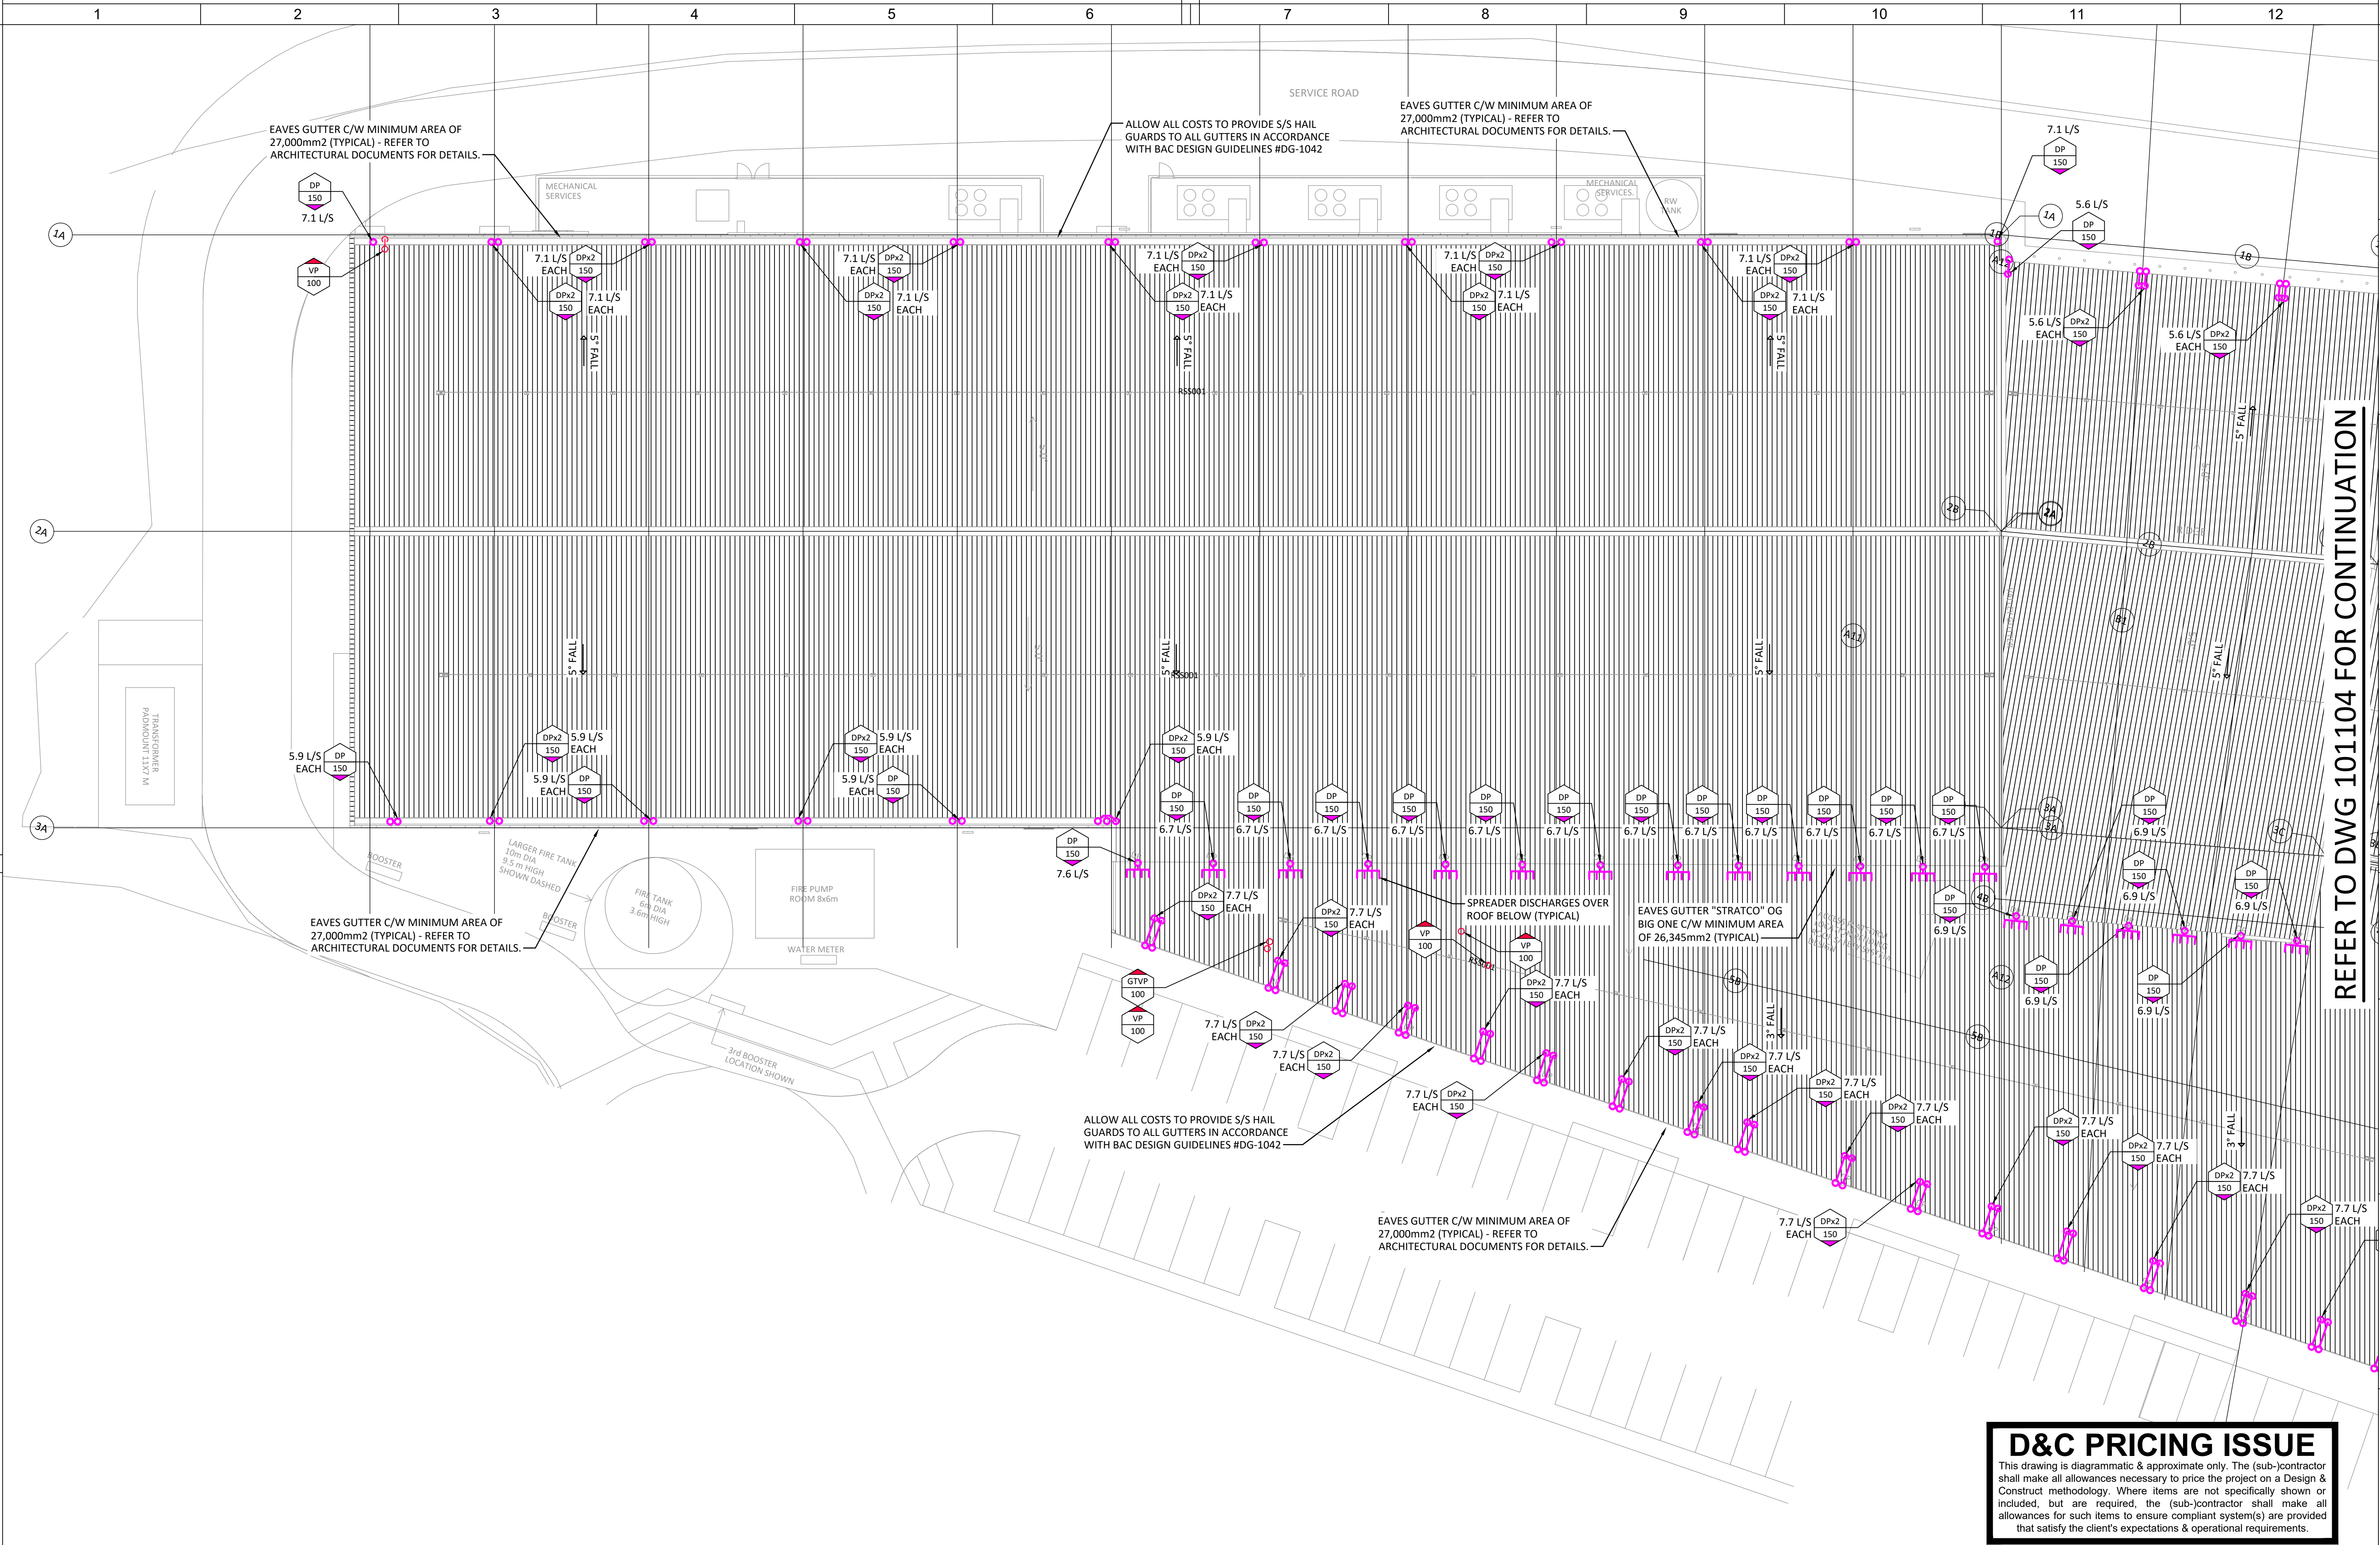

## D&C PRICING ISSUE

This drawing is diagrammatic & approximate only. The (sub-)contractor shall make all allowances necessary to price the project on a Design & Construct methodology. Where items are not specifically shown or included, but are required, the (sub-)contractor shall make all allowances for such items to ensure compliant system(s) are provided that satisfy the client's expectations & operational requirements.

| |
|---|
| COPYRIGHT :<br>REPRODUCTION OF WHOLE OR PART OF<br>THIS DOCUMENT CONSTITUTES AN<br>INFRINGEMENT OF COPYRIGHT. THE<br>INFORMATION, IDEAS AND CONCEPTS<br>CONTAINED IN THIS DOCUMENT ARE<br>CONFIDENTIAL. THE RECIPIENT(S) OF THIS<br>DOCUMENT IS PROHIBITED FROM<br>DISCLOSING SUCH INFORMATION IDEAS<br>AND CONCEPTS TO ANY PERSON WITHOUT<br>THE PRIOR WRITTEN CONSENT OF THE<br>BRISBANE AIRPORT CORPORATION PTY. LTD | |
|---|