



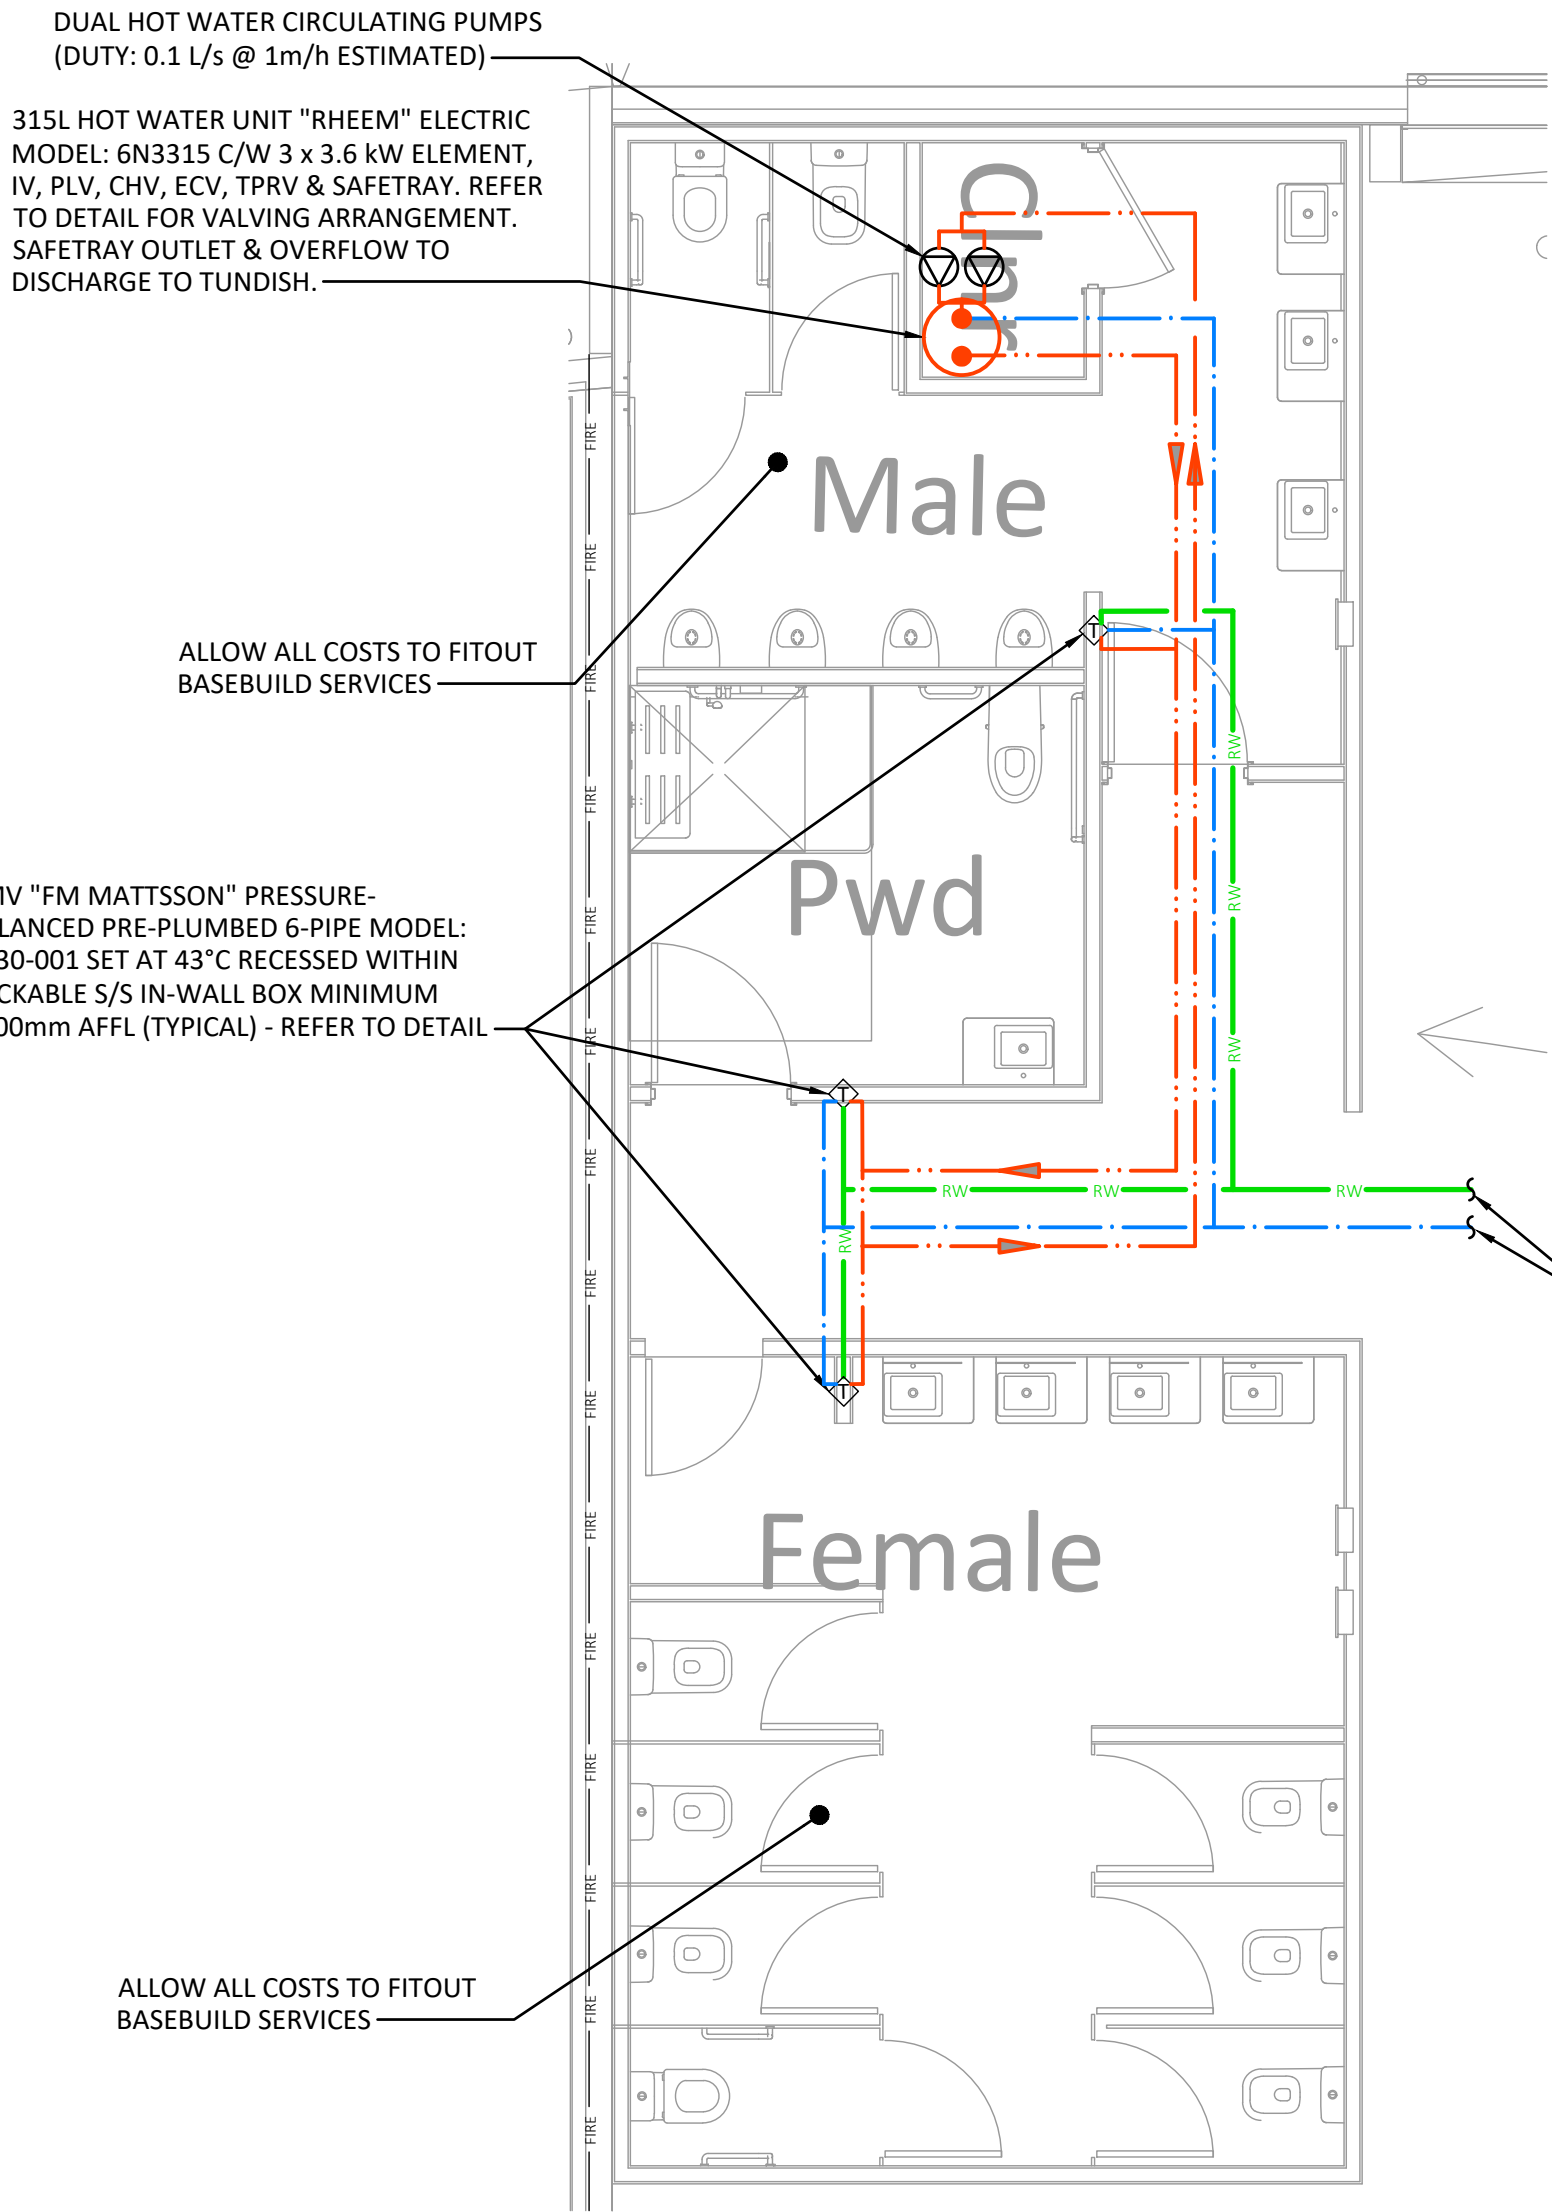

AMENITIES - TENANCY 2  
SCALE 1:50

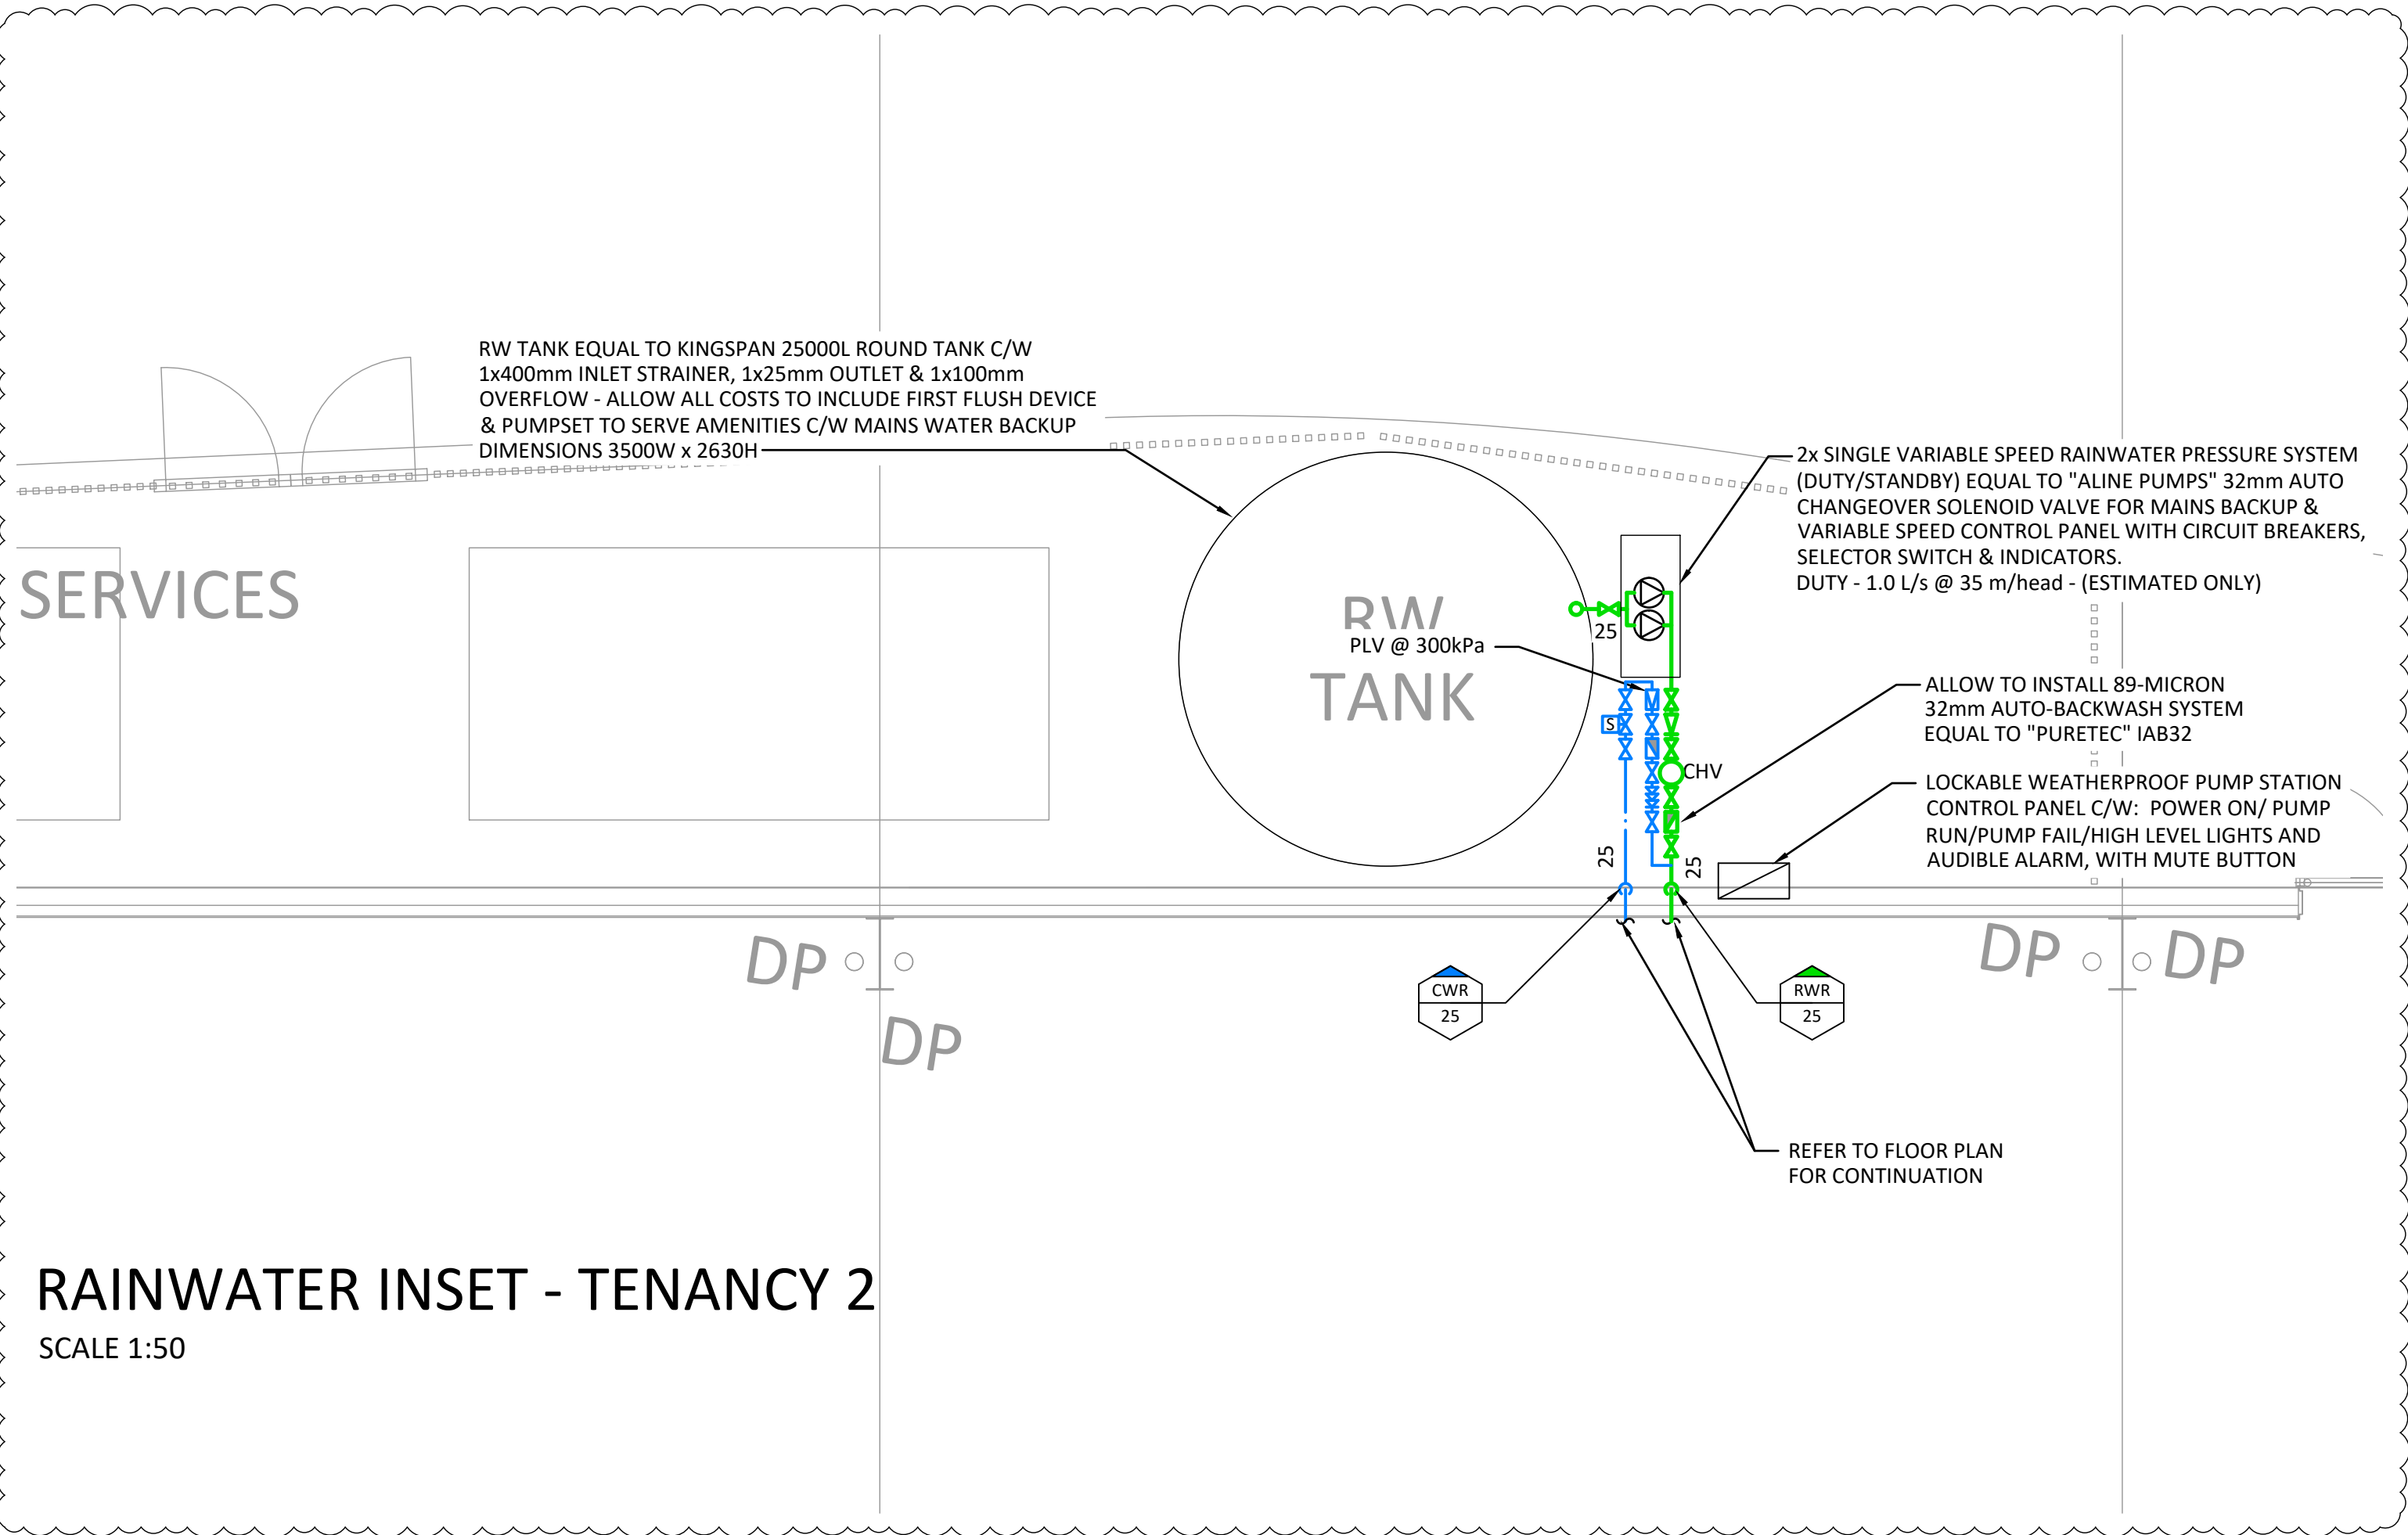

RAINWATER INSET - TENANCY 2  
SCALE 1:50

### D&C PRICING ISSUE

This drawing is diagrammatic & approximate only. The (sub-)contractor shall make all allowances necessary to price the project on a Design & Construct methodology. Where items are not specifically shown or included, but are required, the (sub-)contractor shall make all allowances for such items to ensure compliant system(s) are provided that satisfy the client's expectations & operational requirements.