


Sheet size: A1
Drawing to be printed in colour
Drawing © Northrop Consulting Engineers Pty Ltd.

DESIGN NOTES AND ASSUMPTIONS:
HIGH LEVEL FOUNDATIONS HAVE BEEN DESIGNED FOR A
RESULTANT ALLOWABLE BEARING PRESSURE OF 100kPa.

ALL FOOTINGS TO BE N32 CONCRETE STRENGTH UNO.

ALLOW FOR 600sq x 400d PAD FOOTINGS EITHER SIDE
OF PEDESTRIAN AND ROLLER DOORS.

FOOTING SCHEDULE		
MARK	SIZE	REINFORCEMENT
PF1	2400 x 2000 x 600 DEEP	ALL FOOTINGS TO BE REINFORCED WITH: DRAMIX 4D 65/60BG @25kg/m3 OR TWINTEC AFT+09/60HE @25kg/M3
PF2	3000 x 2400 x 600 DEEP	
PF3	1800 x 1800 x 400 DEEP	
PF4	1400 x 1400 x 400 DEEP	
PF5	2200 x 2200 x 800 DEEP	
SF1	1200 W x 400 DEEP	

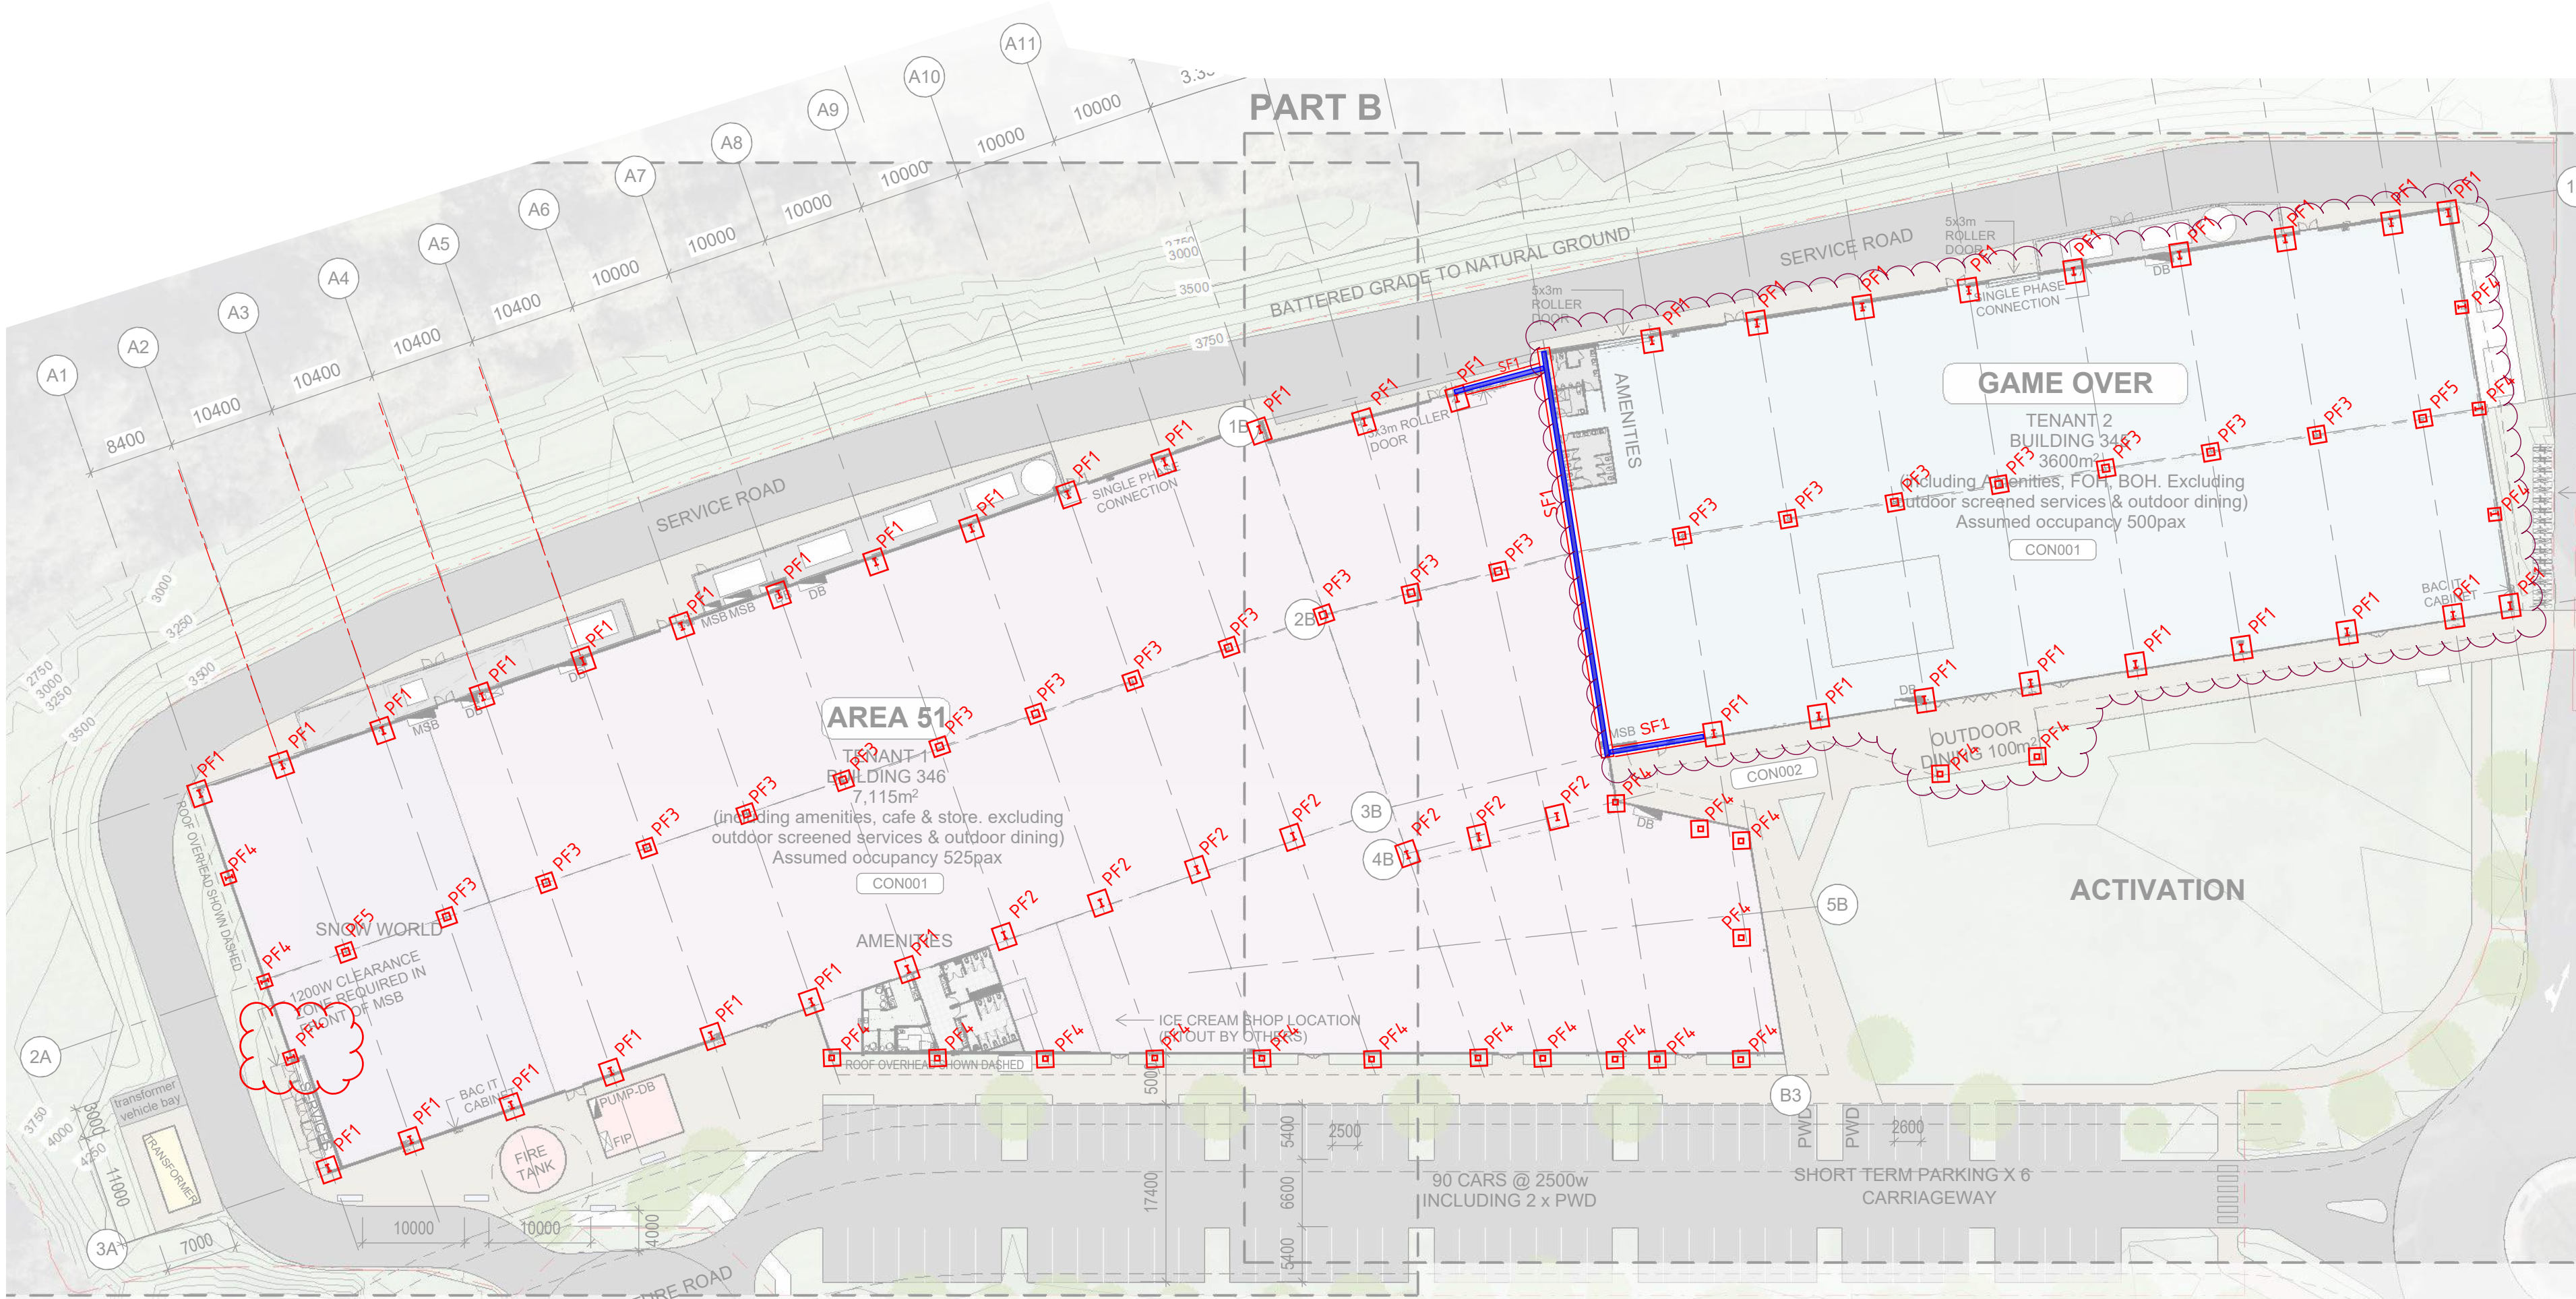

FOOTING PLAN

NOT FOR CONSTRUCTION