

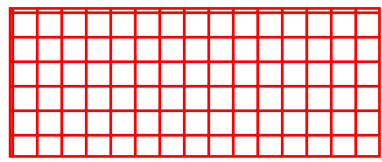


Sheet size: A1
Drawing to be printed in colour
Drawing © Northrop Consulting Engineers Pty Ltd.

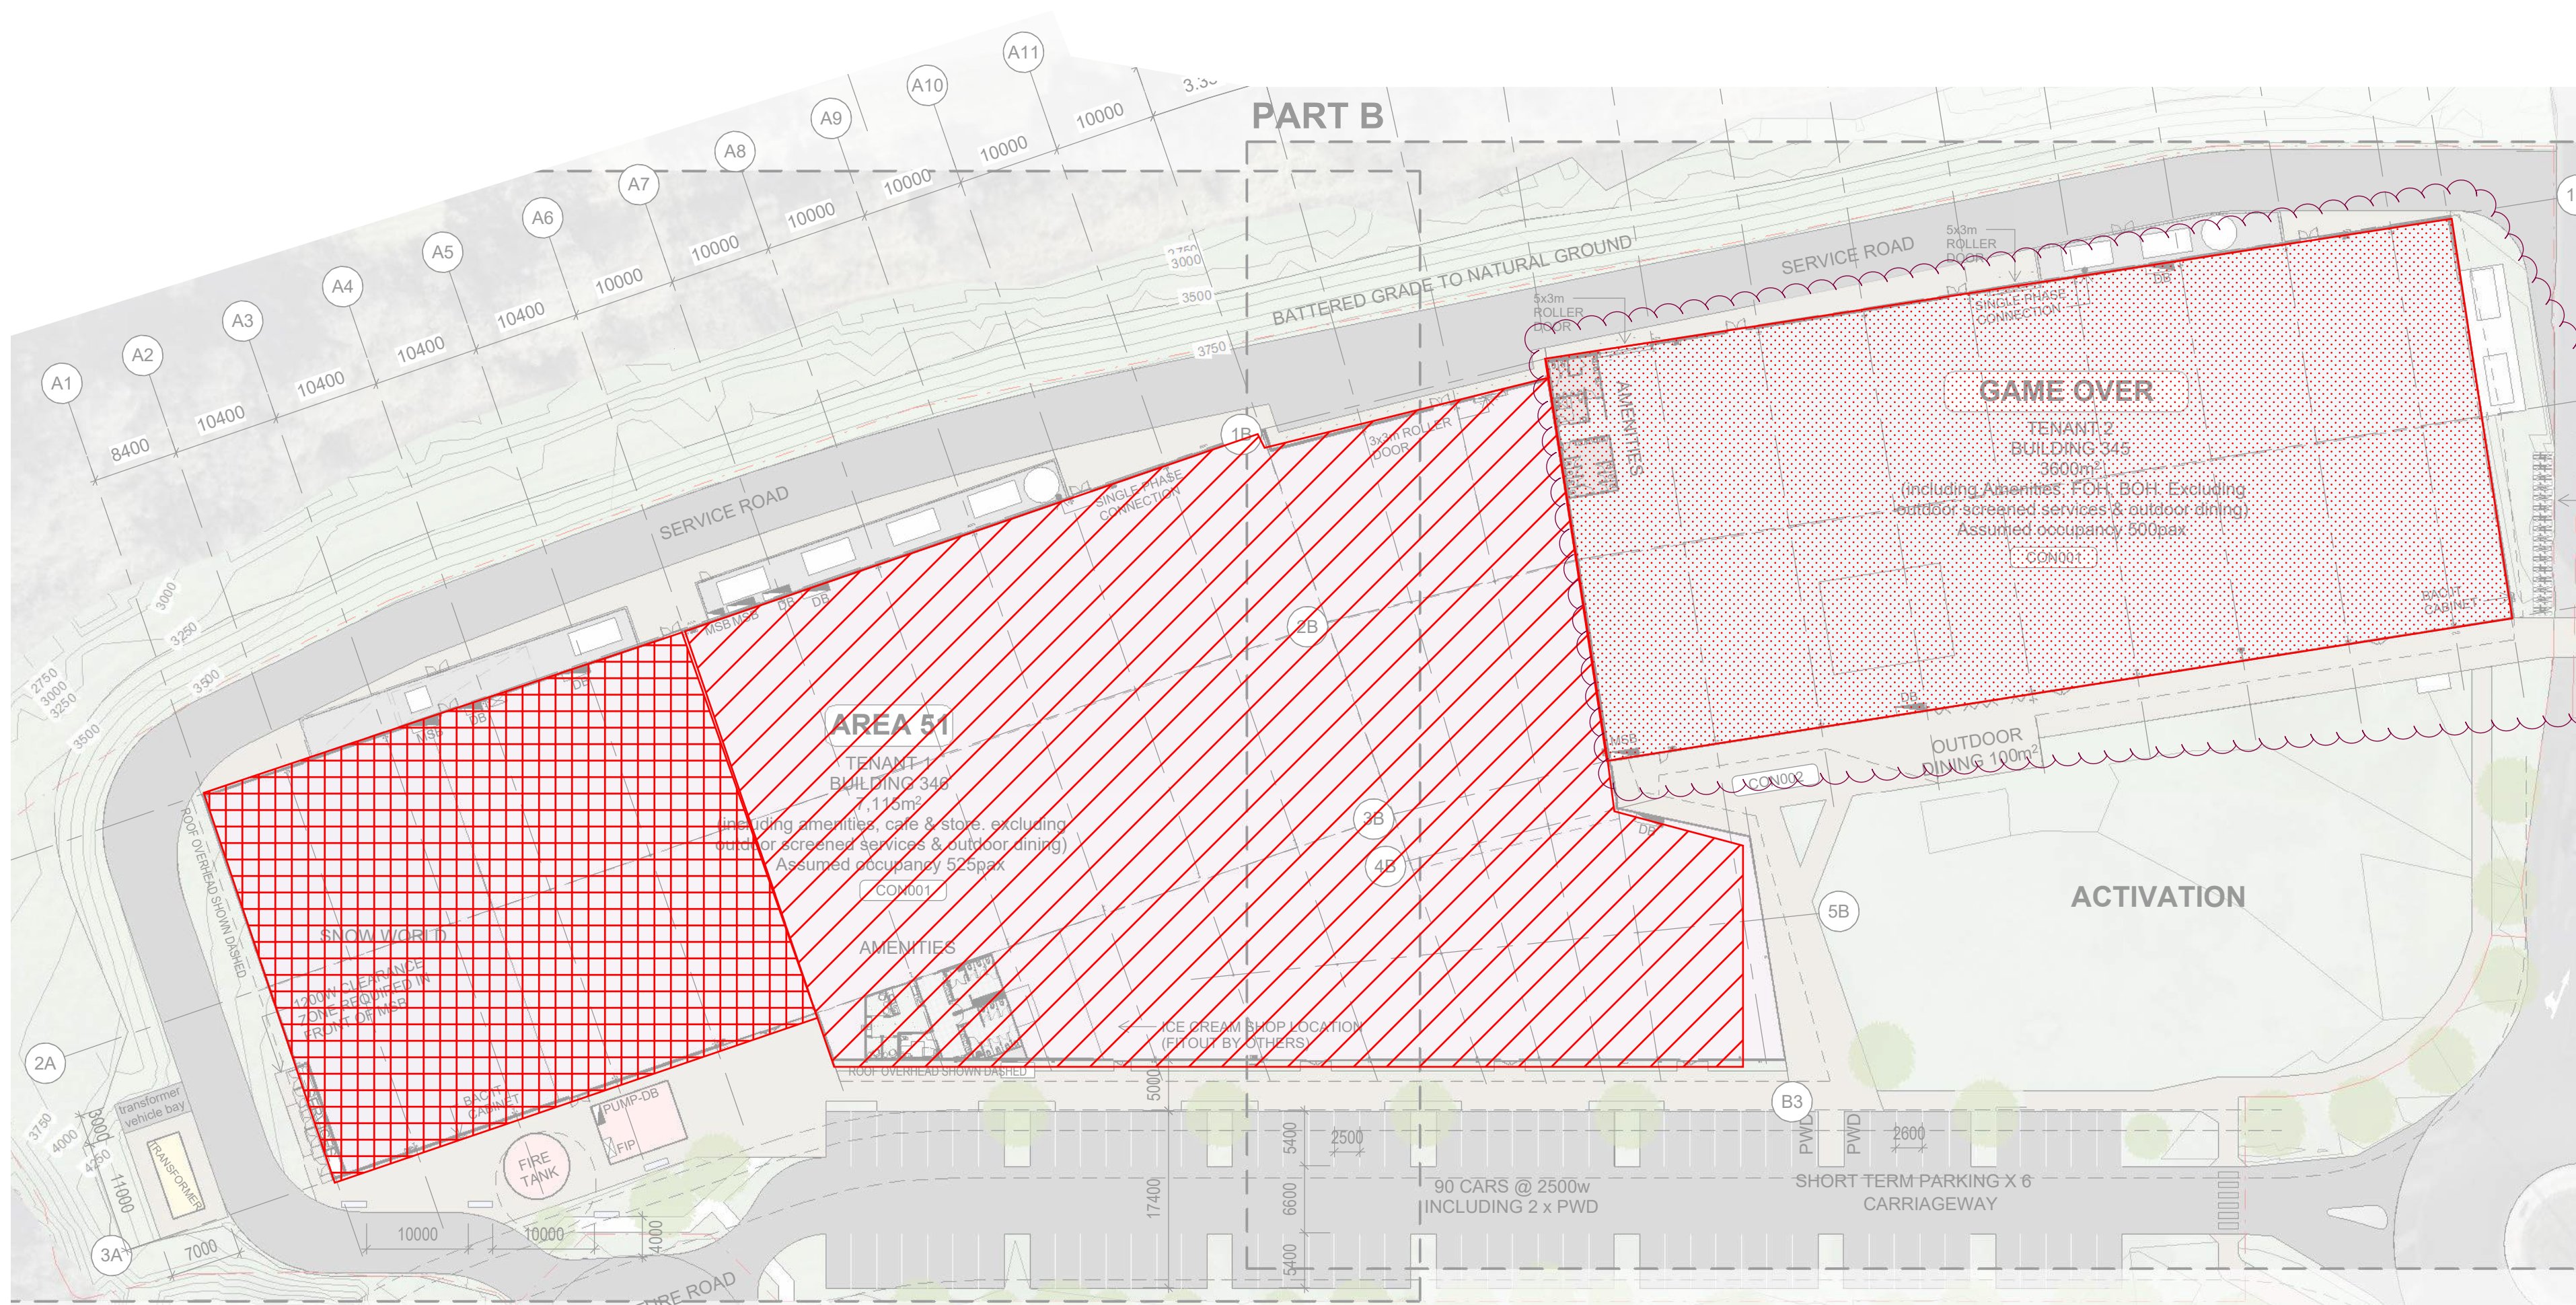


ROOF LOADING - SNOW WORLD
-SDL = 0.5kPa
-SOLAR = 0.15kPa
-LL = 0.25kPa
-Hail = 0.32kPa

Plant locations TBC

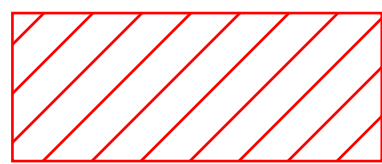

ROOF LOADING - GENERAL AREA 51
-SDL = 0.2kPa
-SOLAR = 0.15kPa
-LL = 0.25kPa
-Hail = 0.32kPa

Plant locations TBC

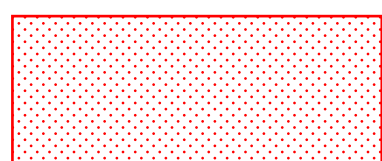

ROOF LOADING - GAME OVER
-SDL = 0.15kPa
-SOLAR = 0.15kPa
-LL = 0.25kPa
-Hail = 0.32kPa

ROOF LOADING PLAN

NOT FOR CONSTRUCTION

NORTHROP

BRISBANE
Level 25, 12 Creek Street
Brisbane City, QLD 4000
brisbane@northrop.com.au
(07) 3365 0400

ABN 81 094 433 100

PARTNERS



Brisbane Airport Corporation Pty Ltd
11 The Circuit Brisbane Airport QLD 4008
PO Box 61 Hamilton QLD 4207 Australia
Telephone : 61 7 3406 3000
Facsimile : 61 7 3406 3111
Email : info@bne.com.au
www.brisbaneairport.com.au
ABN 54 076 870 650

Archipelago

DRAWN

Author

DESIGNED

Designer

1:100
0
5000
0
1:100
Scale at A1

Refer to architect's drawings for setout

JOB MANAGER

Checker

VERIFIER

Approver

REV. DESCRIPTION

REV.	DESCRIPTION	ISSUED	DATE
A	FOR INFORMATION	NS	29/08/25
B	FOR INFORMATION	JS	21/11/25
C	FOR INFORMATION	NS	19/12/25
D	FOR TENDER	NS	04/02/26

PROJECT

BAC BNE SKYGATE PLAY

ADDRESS

DRAWING TITLE

ROOF LOADING PLAN

JOB No.
250946
DRAWING No.
25021-NRP-XX-01-DR-ST-000005

REV.

D