




Sheet size: A1
Drawing to be printed in colour
Drawing © Northrop Consulting Engineers Pty Ltd.

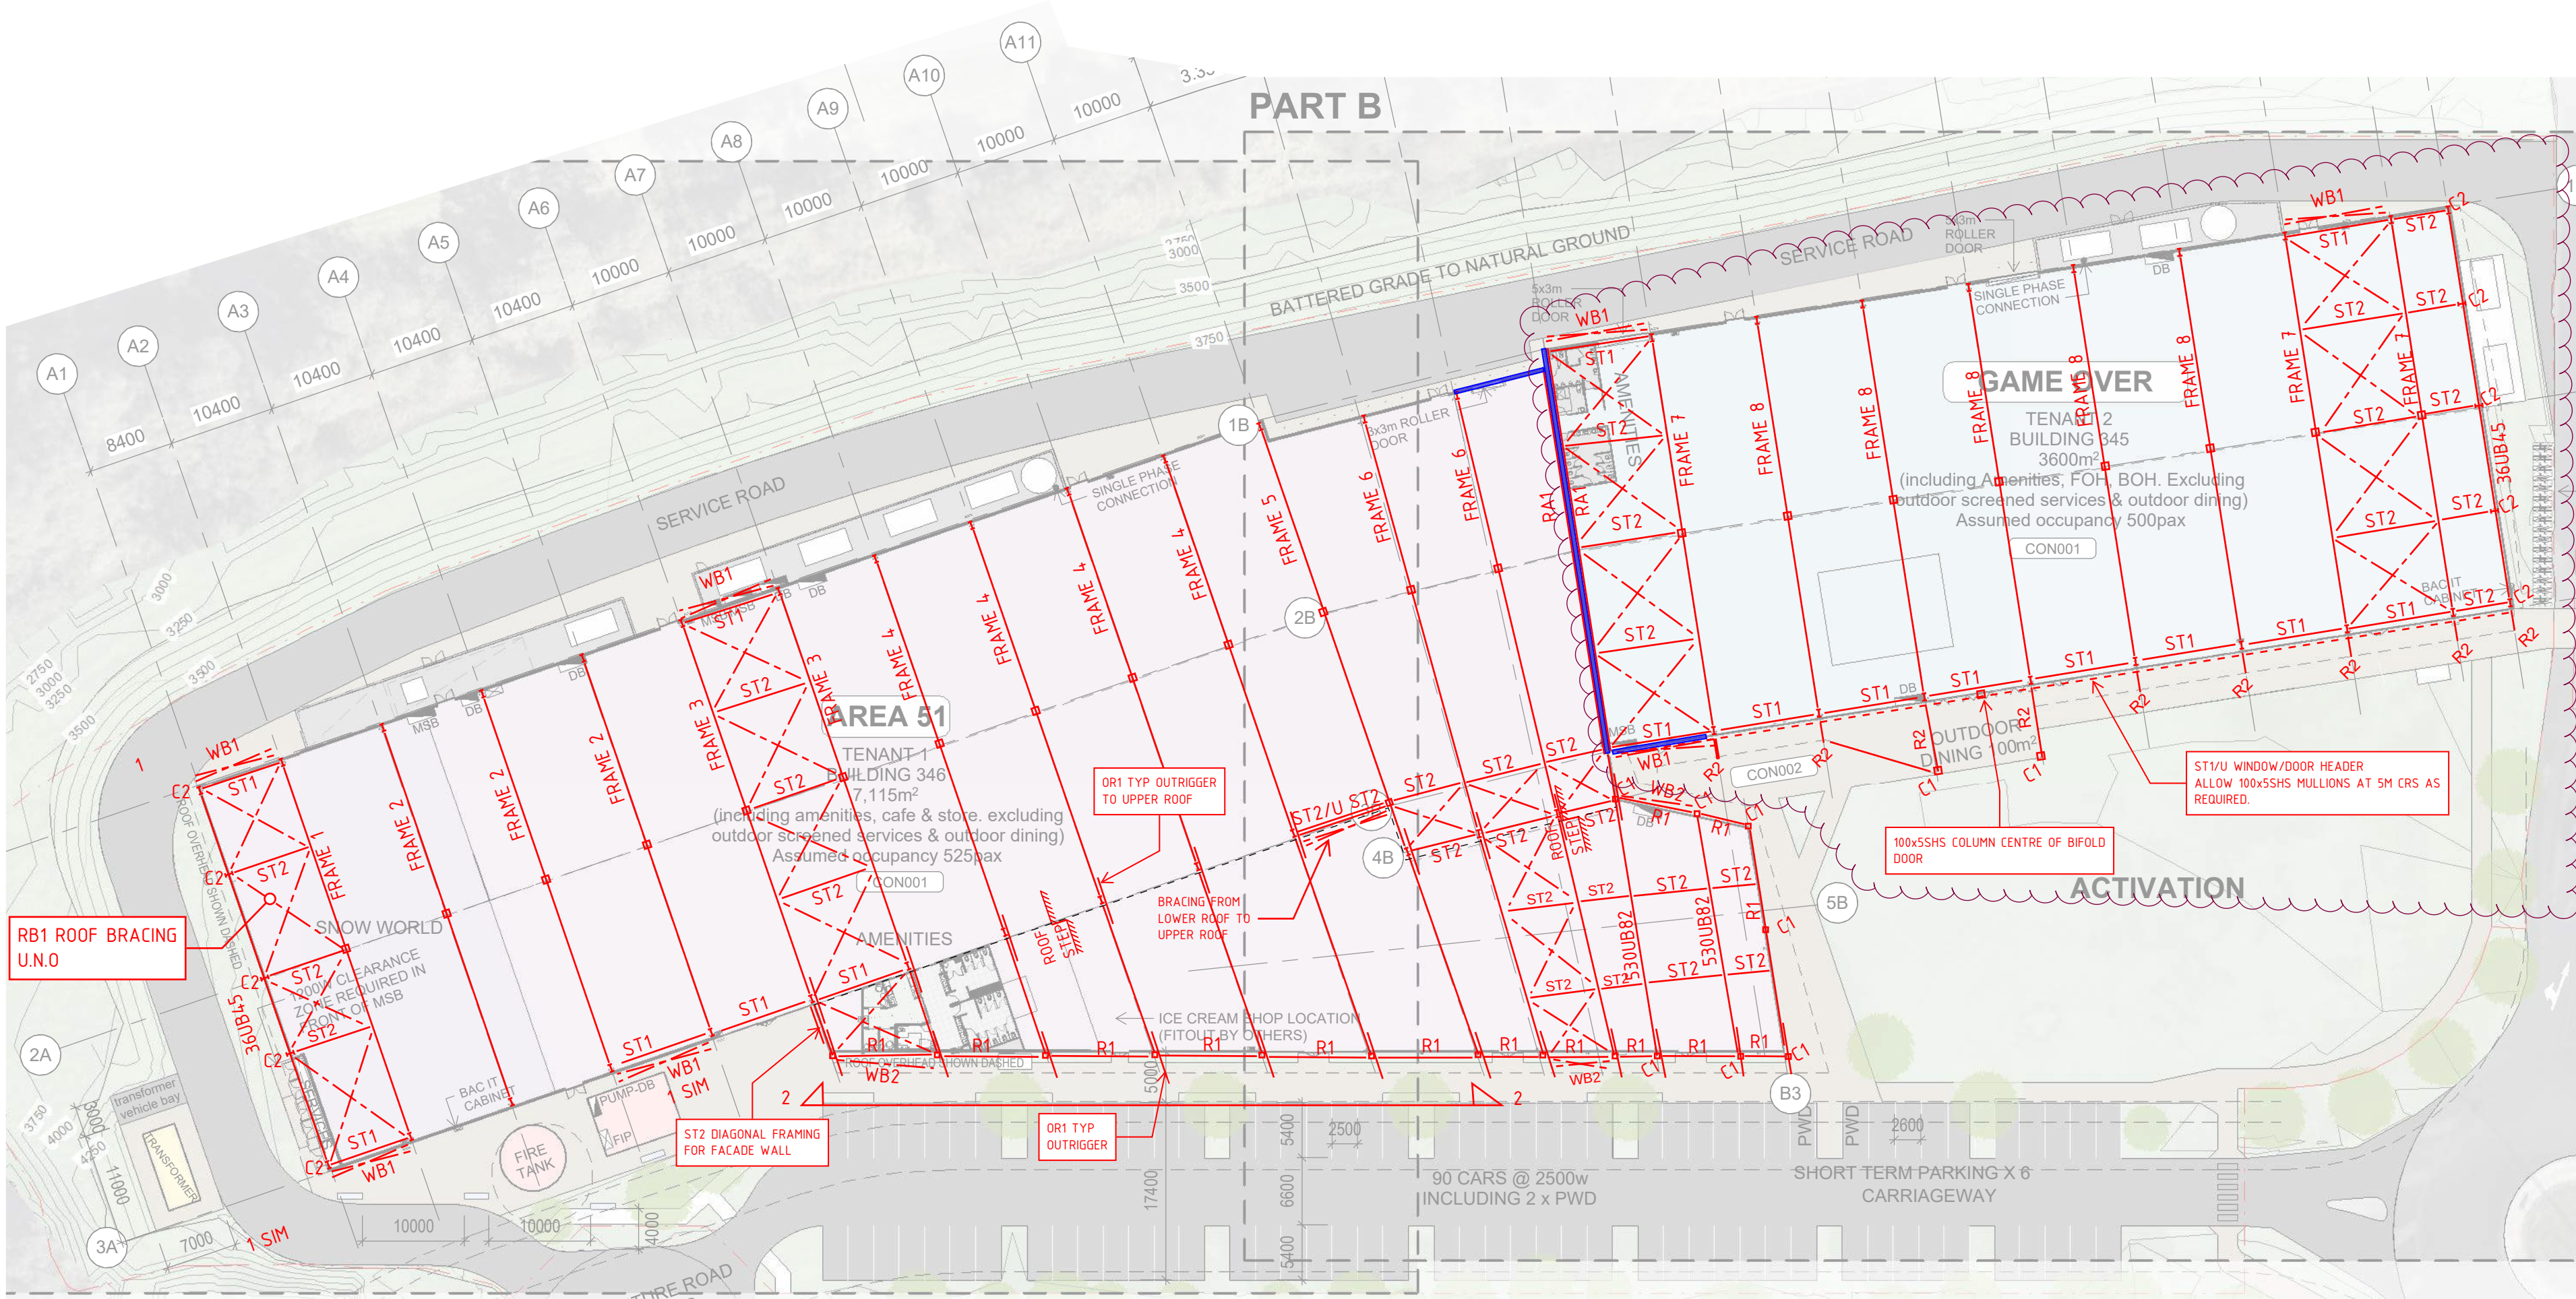

ROOF FRAMING PLAN

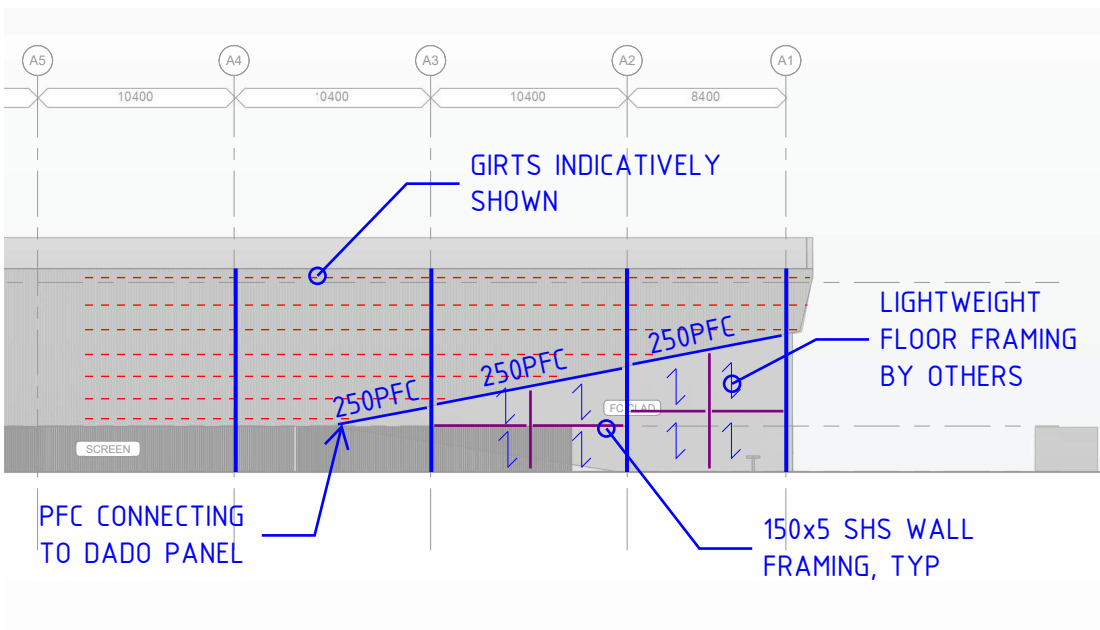

ELEVATION 1

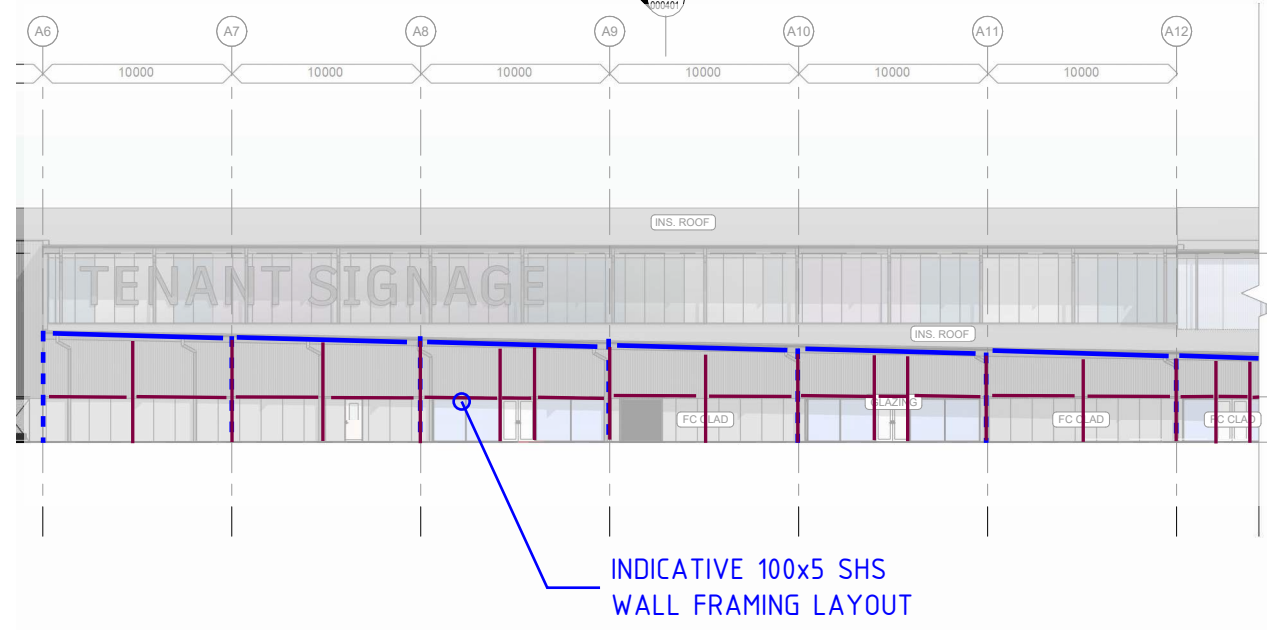

ELEVATION 2

DESIGN NOTES AND ASSUMPTIONS:
DESIGN IS IN ACCORDANCE WITH NCC 2022 AND HENCE
SOLAR LOADING OF 0.15kPa IS APPLIED TO FULL
WAREHOUSE ROOF.

LOADING
AS PER LOADING PLAN

ADDITIONAL ALLOWANCES
FLY BRACING
ALLOW 3 TONNE ADDITIONAL

GIRTS
ALLOW EC25019-900 CTS, 3 ROWS BRIDGING (SINGLE SPAN
BETWEEN COLUMNS TO MATCH ARCH DETAILING)

PLANT PLATFORMS
LOCATIONS IN AREA 51 TBC. ADDITIONAL STEELWORK TO
PORTAL FRAMES AND PLATFORMS THEMSELVES WILL NEED
TO BE ALLOWED FOR

WINDOW FRAMING TO AREA 51 LOWER AREA
ALLOW 100X5 SHS MULLIONS @ 5M CRS ALONG EXTERNAL
WALL.

DADO PANELS
150 THICK, 2400 ABOVE FFL TYP, 3000 AT ALL HYDRANTS
N32, SL82 CENTRAL MESH, N16 PERIMETER BARS
ALLOW 15kg/m2 ADDITIONAL LOOSE BAR

GREENSTAR NOTE:
IN ORDER TO MEET GREENSTAR PATHWAY STRUCTURAL
STEEL SUPPLIER MUST ACHIEVE LEVEL 2 OR 3 CERTIFIED
UNDER 'STEEL SUSTAINABILITY AUSTRALIA'

MEMBER SCHEDULE

BR1 – 75x75x8 EA
WB1 – 75x75x8 EA
WB2 – 89x6 SHS

ST1 – 200x6 SHS
ST2 – 150x5 SHS
ST3 – 125x5 SHS

R1 – 300PFC
R2 – 250PFC

RA1 – 90x90x8 EA

C1 – 150x5 SHS
C2 – 410UB54

OR1 – 250PFC

TB1 – 610UB101
TB2 – 530UB82

FRAMES – REFER ELEVATIONS

..... DENOTES ST2 AT 4M SPACING MAX
TO SUPPORT ARCHITECTURAL
SCREENS

NOT FOR CONSTRUCTION

NORTHROP

BRISBANE
Level 25, 12 Creek Street
Brisbane City, QLD 4000
brisbane@northrop.com.au
(07) 3365 0400

PARTNERS
Brisbane
Airport

Brisbane Airport Corporation Pty Ltd
11 The Circuit Brisbane Airport QLD 4008
PO Box 61 Hamilton QLD 4207 Australia
Telephone : 61 7 3406 3000
Facsimile : 61 7 3406 3111
Email : info@bne.com.au
www.brisbaneairport.com.au
ABN 54 076 870 650

Archipelago

DRAWN
Author
DESIGNED
Designer

1:100
0
5000
0
5000
1:100
Scale at A1 Refer to architect's drawings for setout

JOB MANAGER
Checker
VERIFIER
Approver

REV. DESCRIPTION
A FOR INFORMATION
B FOR INFORMATION
C FOR INFORMATION
D FOR TENDER

ISSUED
NS
JS
NS
NS

DATE
29/08/25
21/11/25
19/12/25
04/02/26

PROJECT
BAC BNE SKYGATE PLAY

ADDRESS

DRAWING TITLE
ROOF FRAMING PLAN

JOB No.
250946
DRAWING No.
25021-NRP-XX-01-DR-ST-000006

REV.
D