


Drawing © Northrop Consulting Engineers Pty Ltd. Drawing to be printed in colour. Sheet size: A1

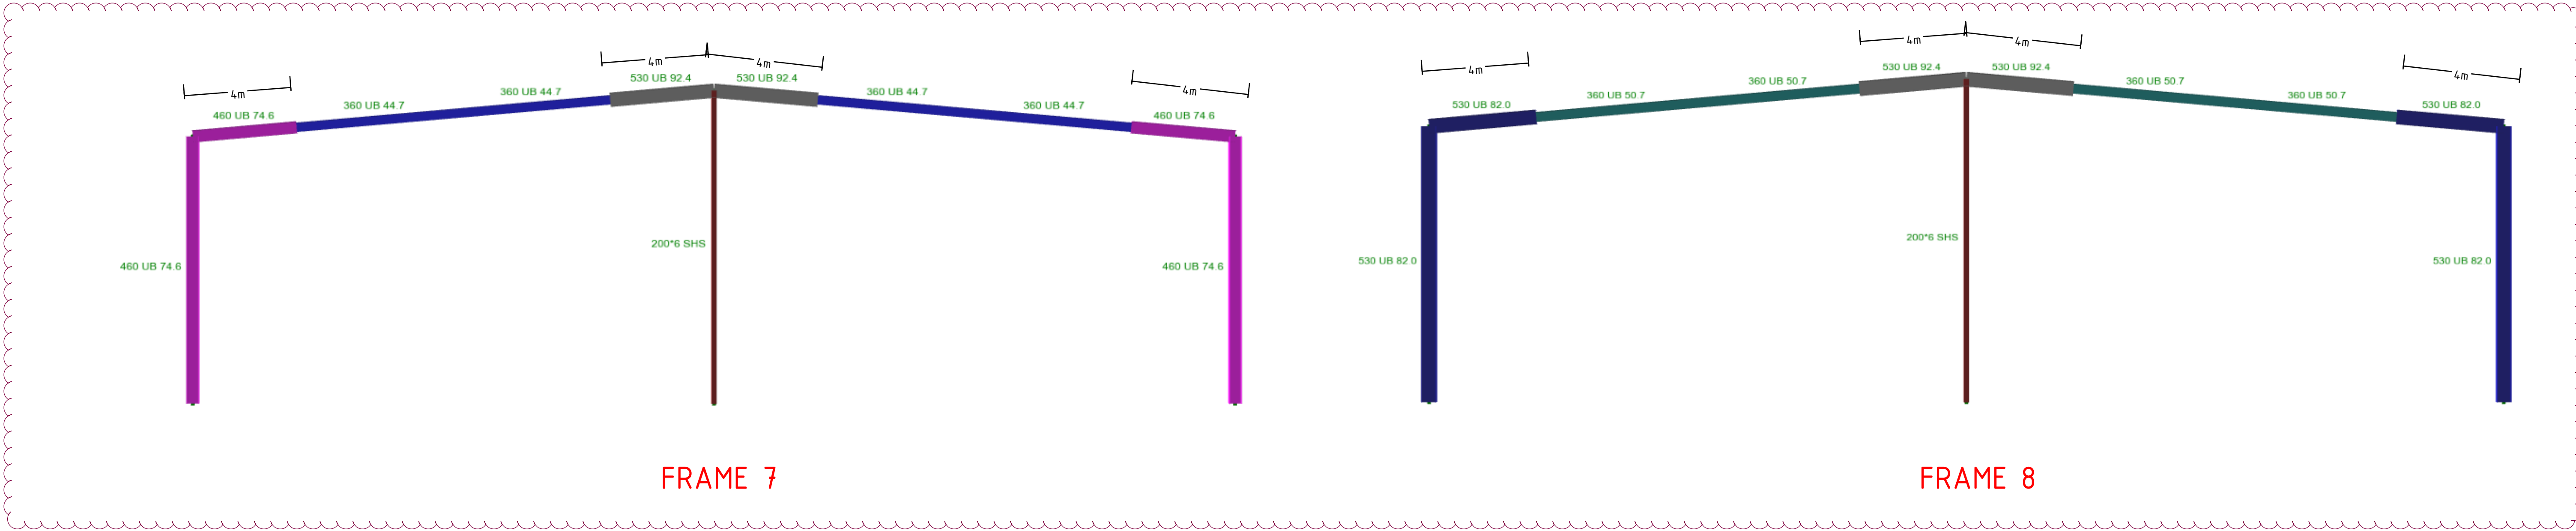

NOT FOR CONSTRUCTION

NORTHROP

PARTNERS



Brisbane Airport

Brisbane Airport Corporation Pty Ltd
11 The Circuit Brisbane Airport QLD 4008
PO Box 61 Hamilton QLD 4207 Australia
Telephone : 61 7 3406 3000
Facsimile : 61 7 3406 3111
Email : info@bne.com.au
www.brisbaneairport.com.au
ABN 54 076 870 650

Archipelago

DRAWN

JOB MANAGER

DESIGNED

VERIFIER

Scale at A1 Refer to architect's drawings for setout

REV.	DESCRIPTION	ISSUED	DATE
A	FOR INFORMATION	NS	29/08/25
B	FOR INFORMATION	JS	21/11/25
C	FOR INFORMATION	NS	19/12/25
D	FOR TENDER	NS	04/02/26

PROJECT

BAC BNE SKYGATE PLAY

ADDRESS

DRAWING TITLE

PORTAL FRAME ELEVATIONS

SHEET 2

JOB No.

250946

DRAWING No.

25021-NRP-XX-01-DR-ST-000008

ABN 81 094 433 100

REV.
D