


THIS PLAN CARRIES BRISBANE AIRPORT CORPORATION PTY. LTD. (BAC) COPYRIGHT AND IS SUPPLIED FOR INFORMATION ONLY. THIS PLAN MUST BE VERIFIED FOR ACCURACY AND COMPLETENESS BY NECESSARY INVESTIGATION, SITE INSPECTION AND MEASUREMENT. THE INFORMATION CONTAINED ON THIS PLAN AND ANY ASSOCIATED DISCUSSIONS, THIS PLAN REMAINS PRELIMINARY IN STATUS UNLESS ALL SIGNATURES HAVE BEEN APPENDED. DO NOT SCALE DRAWING. USE FIGURED DIMENSIONS ONLY.

ALL DIMENSIONS ARE IN METRIC SYSTEM. FOR THE SAKE OF CLARITY, SOME UNDERGROUND SERVICES MAY BE DEPICTED AS SINGLE LINES AND UNLESS OTHERWISE STATED, VALUES OF PSM 31 LOCATED NEAR THE INTERSECTION OF THE RUNWAYS AT THE OLD SUBTRACT 1:154 FROM AERODROME. ALL DRAWINGS PRODUCED BY BAC ARE IN MICROSTATION DGN FORMAT, THEREFORE NO WARRANTIES ARE MADE FOR DIFFERENCES BETWEEN THE DGN FILES AND THE PRINTED DRAWING. ANY OTHER CAD SYSTEMS OR WITHOUT THE NECESSARY MICROSTATION RESOURCE FILES.

BAC HAS ENTERED INTO A LICENCE AGREEMENT WITH AEROMETREX LTD TO USE CERTAIN MAPS (IE FROM APT) OF THE AIRPORT CORP. PRODUCT. YOU MAY ONLY USE, COPY OR DISTRIBUTE THE PRODUCT FOR BAC INTERNAL BUSINESS PURPOSES. YOU UNDERTAKE TO DESTROY OR RETURN TO BAC ANY AND ALL COPIES OF THE PRODUCT WHICH ARE WITHIN YOUR POSSESSION, CUSTODY OR CONTROL WHEN YOU NO LONGER REQUIRE THEM FOR BAC INTERNAL BUSINESS PURPOSES.

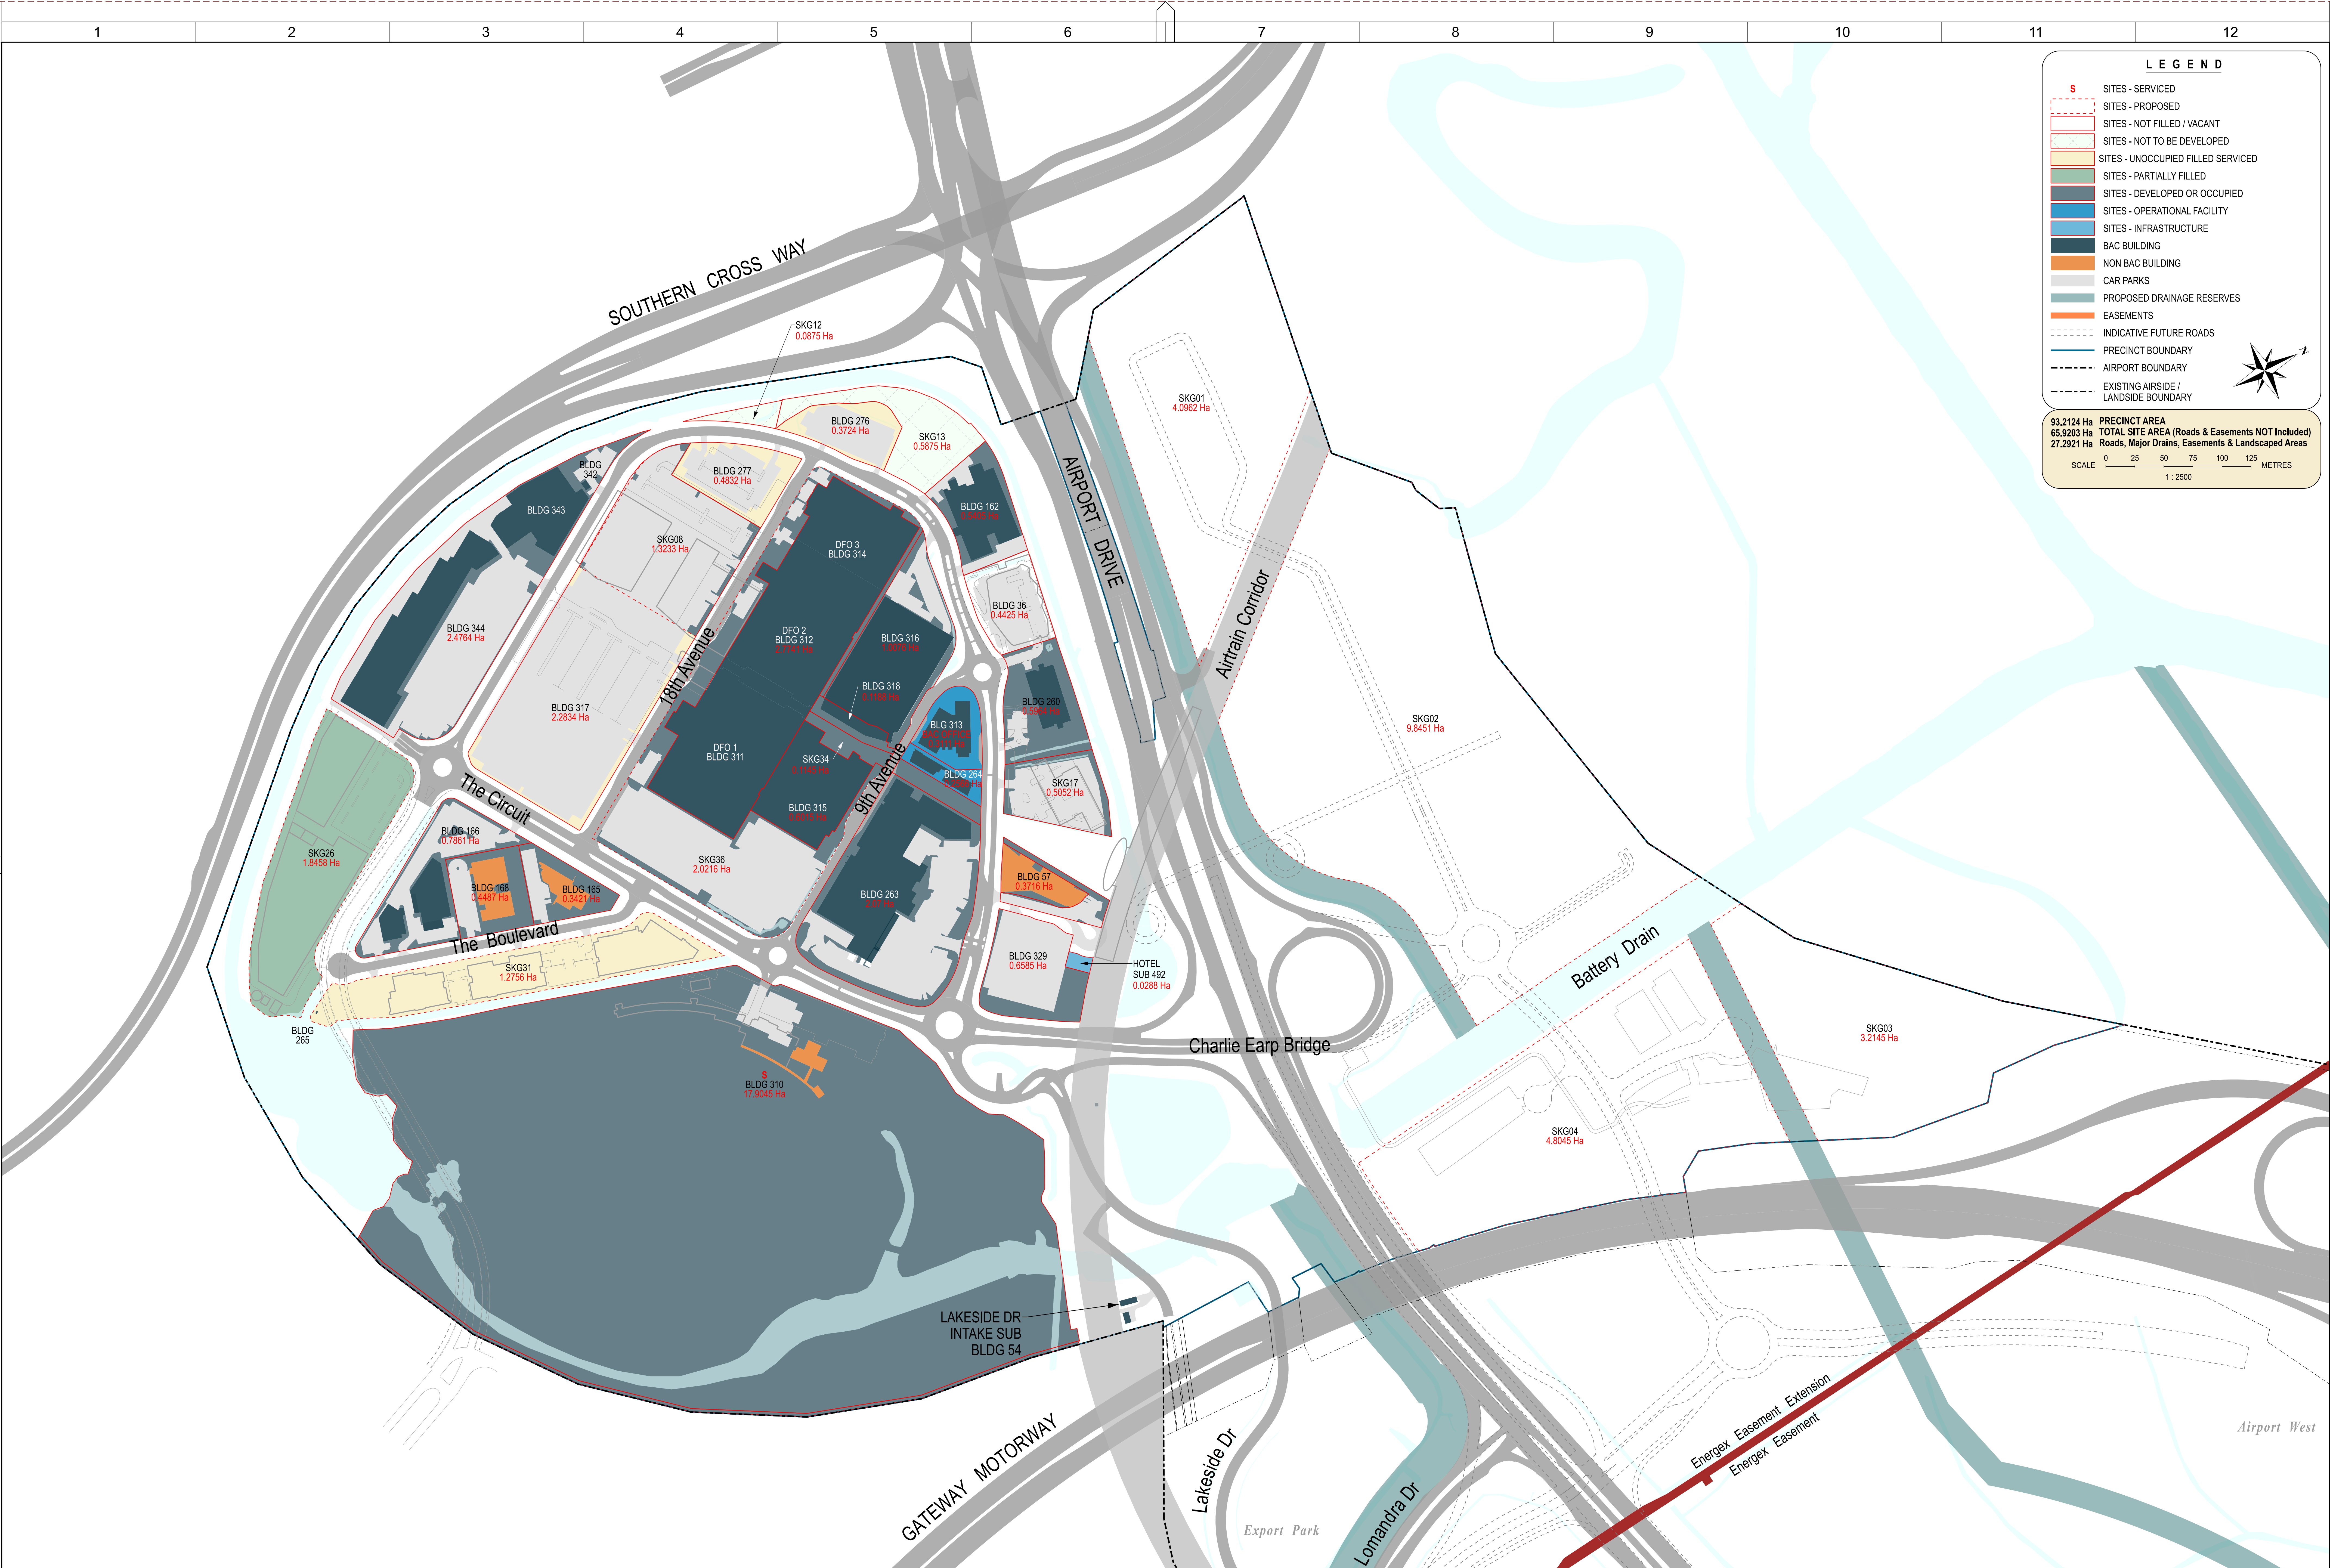

255421	JES	ADDED SCHNEIDER ROAD EXTENDING INTO SKYGATE SOUTH OF GOLF CENTRAL.	21/05/25	45
255130	JES	AMENDED SKG26 TO SUIT NEW DESIGN LAYOUT.	08/04/25	44
44923	JES	SLIGHT ADJUSTMENT TO BLDG 317 AREA AROUND SKG08.	18/07/22	43
42906	JES	SG8 & 36 NOW OCCUPIED. BLDG 36 VACANT. SG12 & 13 CHANGED TO NOT TO BE	19/04/21	42
42906	JES	DEVELOPED. BLDG 313 & 264 CHANGED TO OPERATIONAL. HOTEL SUB 492	19/04/21	42
42906	JES	CHANGED TO INFRASTRUCTURE. PROPOSED BLDG 57 AREA SHOWN AS EXISTING.	19/04/21	42
42906	JES	RENAMED ALL SITES FROM SG TO SKG.	19/04/21	42
Req. No.	Drawn	Amendment	Date	Rev. No.

Authorised Rep. & Signature	Date
Authorised Rep. & Signature	Date
Checked By	Date

PRECINCT LOT PLAN
SKYGATE

		BRISBANE AIRPORT CORPORATION PTY LTD 11 THE CIRCUIT, BRISBANE AIRPORT QLD 4008 PO BOX 81, HAMILTON CENTRAL QLD 4007 AUSTRALIA T +61 73403000 E INFO@BNE.COM.AU W BNE.COM.AU	Scale 1 : 2 500 Size A1 Revision 45
Design Ref.	Project Ref.	Discipline	Airport Precinct
Drg. No.	BAC / 061020 / P / 01	Sub-Number	0001