

1 2 3 4 5 6 7 8 9 10 11 12

A

B

C

D

E


F

G

H

I

J

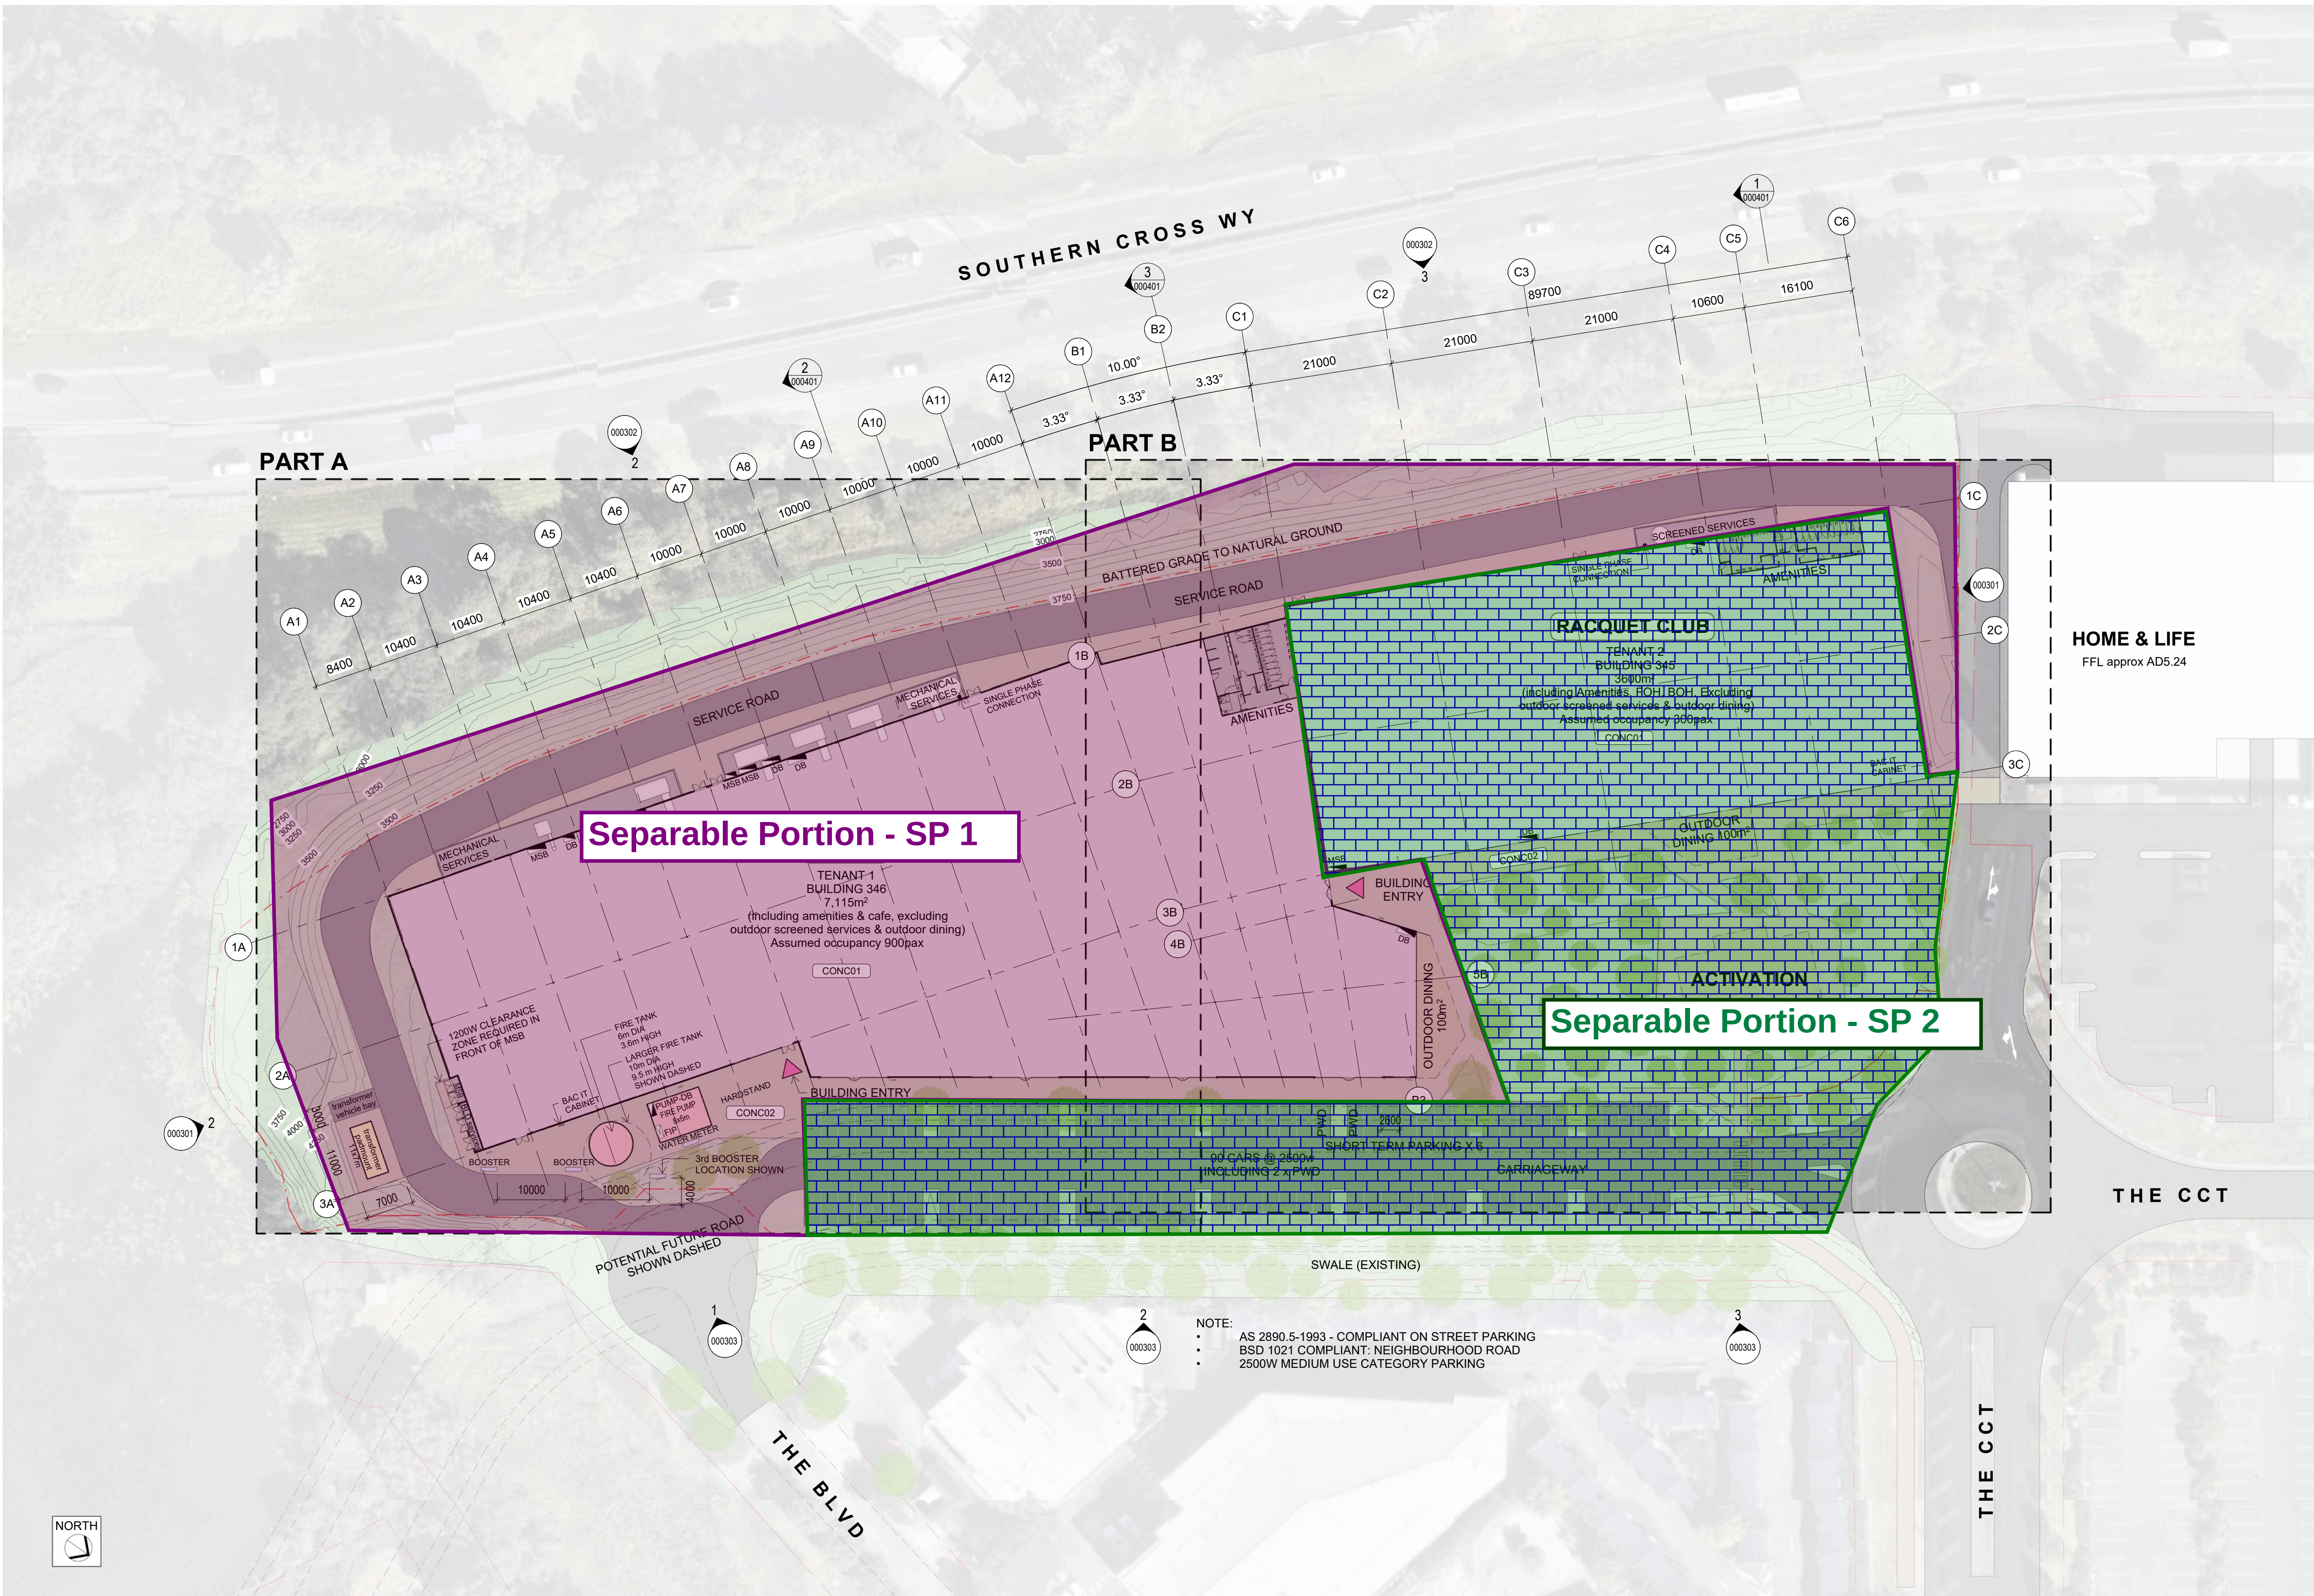

AREA SUMMARY

TENANT 1	
Area 51 (includes amenities & cafe)	7,115m ²
Screened services	300m ²
Outdoor dining	100m ²
TENANT 2	
RACQUET CLUB (includes amenities)	3,600m ²
Screened services	65m ²
Outdoor dining	100m ²

Note: Areas measured are inclusive of external walls

PARKING SUMMARY

90 cars @ 2500 wide (includes 2 x PWD & 6 short term parking)

OCCUPANCY SUMMARY

AREA51
AREA51 BRIEF: 900PAX (STAFF INCLUDED)
NCC CLASS 9B

RACQUET CLUB
RACQUET CLUB BRIEF: 300PAX (STAFF INCLUDED)
NCC CLASS 9B

COPYRIGHT:
REPRODUCTION OF WHOLE OR PART OF THIS DOCUMENT
CONSTITUTES AN INFRINGEMENT OF COPYRIGHT. THE
INFORMATION, IDEAS AND CONCEPTS CONTAINED IN THIS
DOCUMENT ARE CONFIDENTIAL. THE RECIPIENT(S) OF
THIS DOCUMENT IS PROHIBITED FROM DISCLOSING SUCH
INFORMATION IDEAS AND CONCEPTS TO ANY PERSON
WITHOUT THE PRIOR WRITTEN CONSENT OF THE
BRISBANE AIRPORT CORPORATION PTY. LTD.

DRN	AMENDMENTS	DATE	REV
JB	PRELIMINARY WIP ISSUE	25.07.2025	1
DC	WIP TENANCY PLAN	15.08.2025	2
JB	WIP TENANCY PLAN	21.08.2025	3
JB	WIP CONCEPT	22.08.2025	4
JB	QUANTITY SURVEYOR ISSUE	29.08.2025	5
JB	30% DD ISSUE	12.09.2025	6

TAG LEGEND	
COL	COLUMN REFER STR. ENG.
CONC01	CONCRETE SLAB
CONC02	CONCRETE SLAB - EXTERNAL HARDSTAND
DANPALON	DANPALON SINGLE GLAZED TRANSLUCENT CLADDING - REFER TO SECTION J REPORT
DP	DOWNPIPE
FC CLAD	PREFINISHED FC SHEET CLADDING - REFER TO SECTION J REPORT
FH	DOUBLE PILLAR FIRE HYDRANT REFER HYD. ENG.
GLAZING	POWDERCOATED ALUMINIUM FRAMED COMMERCIAL GLAZING
PRE_CONC	PRECAST CONCRETE DADO WALLS
SCREEN	POWDERCOATED ALUMINIUM BATTEN SCREENING

Archipelago

Archipelago
Level 3, 189 George Street, Brisbane QLD 4000
T +617 3236 4806 www.archipelago.com.au
© ARCHIPELAGO ARCHITECTS PTY. LTD. All Rights Reserved
This work is copyright and cannot be reproduced or copied by any means without written permission of Archipelago Architects Pty Ltd. Any
license, express or implied, to use this document for any purpose
whatsoever is restricted to the terms of the agreement between Archipelago Architects P
y Ltd and the instructing party.

SKYGATE PLAY

TENANCY PLAN

Drawn JB	Checked DC
Design Coordinated N/A	Compliance Checked N/A
Authorised For Issue DC	Construction Checked N/A

	Brisbane Airport						Brisbane Airport Corporation Pty Ltd 11 The Circuit Brisbane Airport QLD 4008 PO Box 61 Hamilton QLD 4007 Australia	Scale 1 : 500
							Telephone : 61 7 3406 3000 Facsimile : 61 7 3406 3111 Email : info@bne.com.au www.brisbaneairport.com.au	Size A1
							ABN 54 076 870 650	Revision 6
Project No.	Originator	Volume	Level	Type	Discipline	Number		
Drawing No.	25021	ARC	XX	01	DR	AR	000200	