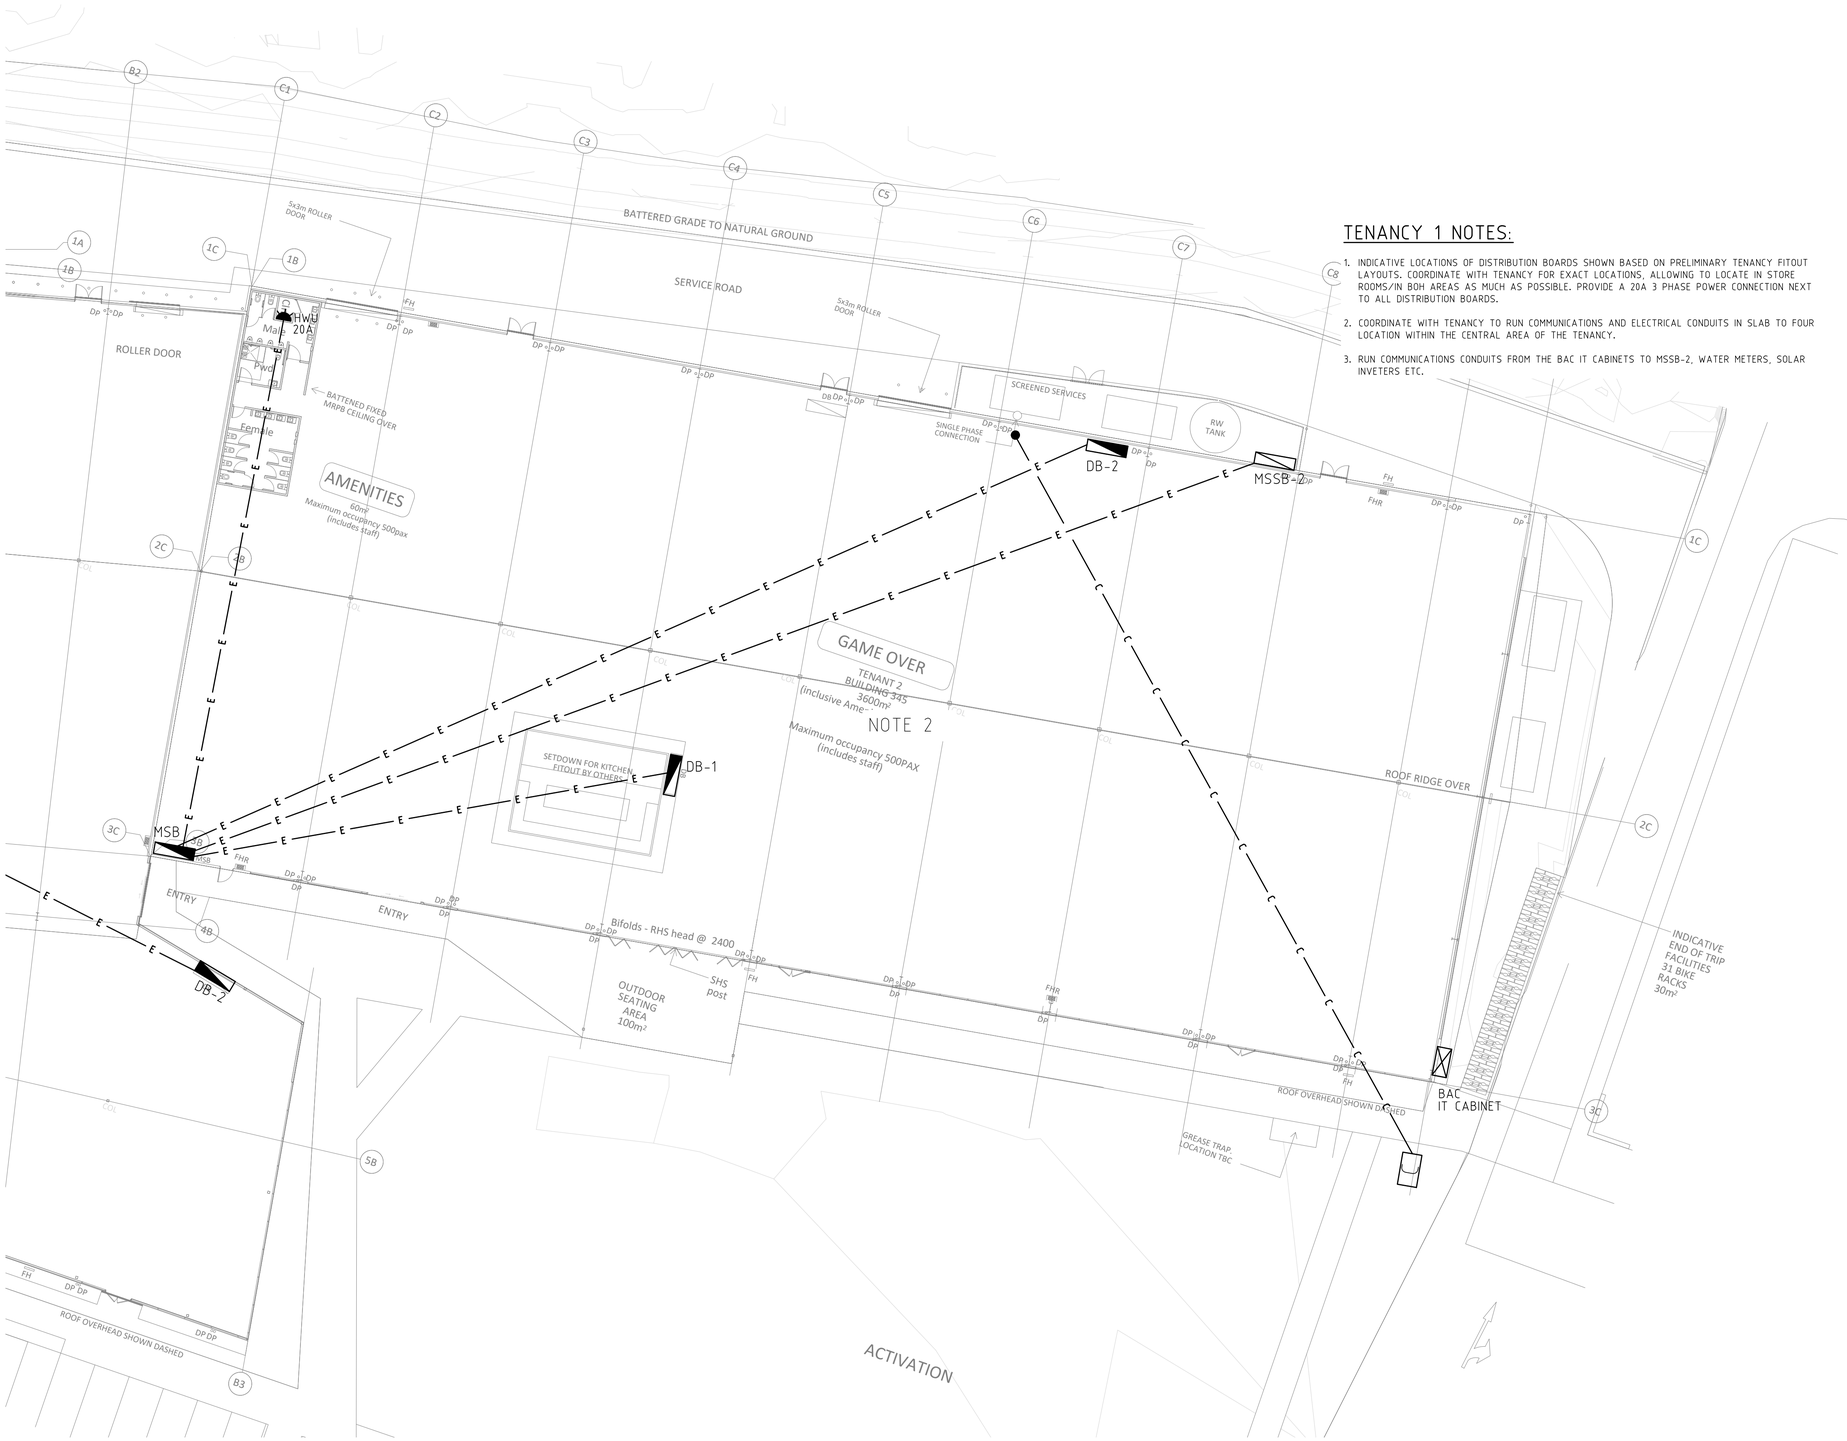


TENANCY 1 NOTES:

1. INDICATIVE LOCATIONS OF DISTRIBUTION BOARDS SHOWN BASED ON PRELIMINARY TENANCY FITOUT LAYOUTS. COORDINATE WITH TENANCY FOR EXACT LOCATIONS, ALLOWING TO LOCATE IN STORE ROOMS/IN BOH AREAS AS MUCH AS POSSIBLE. PROVIDE A 20A 3 PHASE POWER CONNECTION NEXT TO ALL DISTRIBUTION BOARDS.
2. COORDINATE WITH TENANCY TO RUN COMMUNICATIONS AND ELECTRICAL CONDUITS IN SLAB TO FOUR LOCATION WITHIN THE CENTRAL AREA OF THE TENANCY.
3. RUN COMMUNICATIONS CONDUITS FROM THE BAC IT CABINETS TO MSSB-2, WATER METERS, SOLAR INVETERS ETC.

D&C PRICING ISSUE

This drawing is diagrammatic & approximate only. The (sub-)contractor shall make all allowances necessary to price the project on a Design & Construct methodology. Where items are not specifically shown or included, but are required, the (sub-)contractor shall make all allowances for such items to ensure compliant system(s) are provided that satisfy the client's expectations & operational requirements.

client

architect

COPYRIGHT :
REPRODUCTION OF WHOLE OR PART OF THIS DOCUMENT CONSTITUTES AN INFRINGEMENT OF COPYRIGHT. THE INFORMATION, IDEAS AND CONCEPTS CONTAINED IN THIS DOCUMENT ARE CONFIDENTIAL. THE RECIPIENT(S) OF THIS DOCUMENT IS PROHIBITED FROM DISCLOSING SUCH INFORMATION IDEAS AND CONCEPTS TO ANY PERSON WITHOUT THE PRIOR WRITTEN CONSENT OF THE BRISBANE AIRPORT CORPORATION PTY. LTD.

DRN	AMENDMENTS	DATE	REV
RA	D&C PRICING ISSUE	04/02/26	B
RA	D&C PRICING ISSUE	17/12/25	A

25-0437

Ashburner Francis
Ashburner Francis Pty Ltd ABN 46 009 975 197
T 07 3510 8888
E brisbane@ashburnerfrancis.com.au
977 Stanley Street East, East Brisbane QLD 4169
BRISBANE | TOOWOOMBA | TOWNSVILLE | DARWIN
ELECTRICAL SERVICES

Archipelago
Archipelago
Level 3, 199 George Street, Brisbane QLD 4000
T +617 3236 4606 www.archipelago.com.au
© ARCHIPELAGO ARCHITECTS PTY. LTD. All Rights Reserved
This work is copyright and cannot be reproduced or copied by any means without written permission of Archipelago Architects Pty Ltd. Any license, express or implied, to use this document for any purpose whatsoever is restricted to the terms of the agreement between Archipelago Architects Pty Ltd and the instructing party.

Drawn: RA	Checked:
Design Coordinated: RA	Compliance Checked:
Authorised For Issue: DE	Construction Checked:

SKYGATE PLAY
THE CIRCUIT, BRISBANE AIRPORT

ELECTRICAL SERVICES

GAME OVER POWER LAYOUT

Brisbane Airport Corporation Pty Ltd
11 The Circuit Brisbane Airport QLD 4008
PO Box 61 Hamilton QLD 4007 Australia
Telephone : 61 7 3406 3000
Facsimile : 61 7 3406 3111
Email : info@bne.com.au
www.brisbaneairport.com.au
ABN 54 076 870 650

Scale	Size	Revision
1:200	A1	B

Drawing Number	Project No.	Originator	Volume	Level	Type	Discipline	Number
	25021	ASH	XX	XX	DR	EL	001201

File: 2528 - TMR Depot | Pentable: | Printer: | User: #### | Plot Date & Time: 4/06/2025 7:54 PM